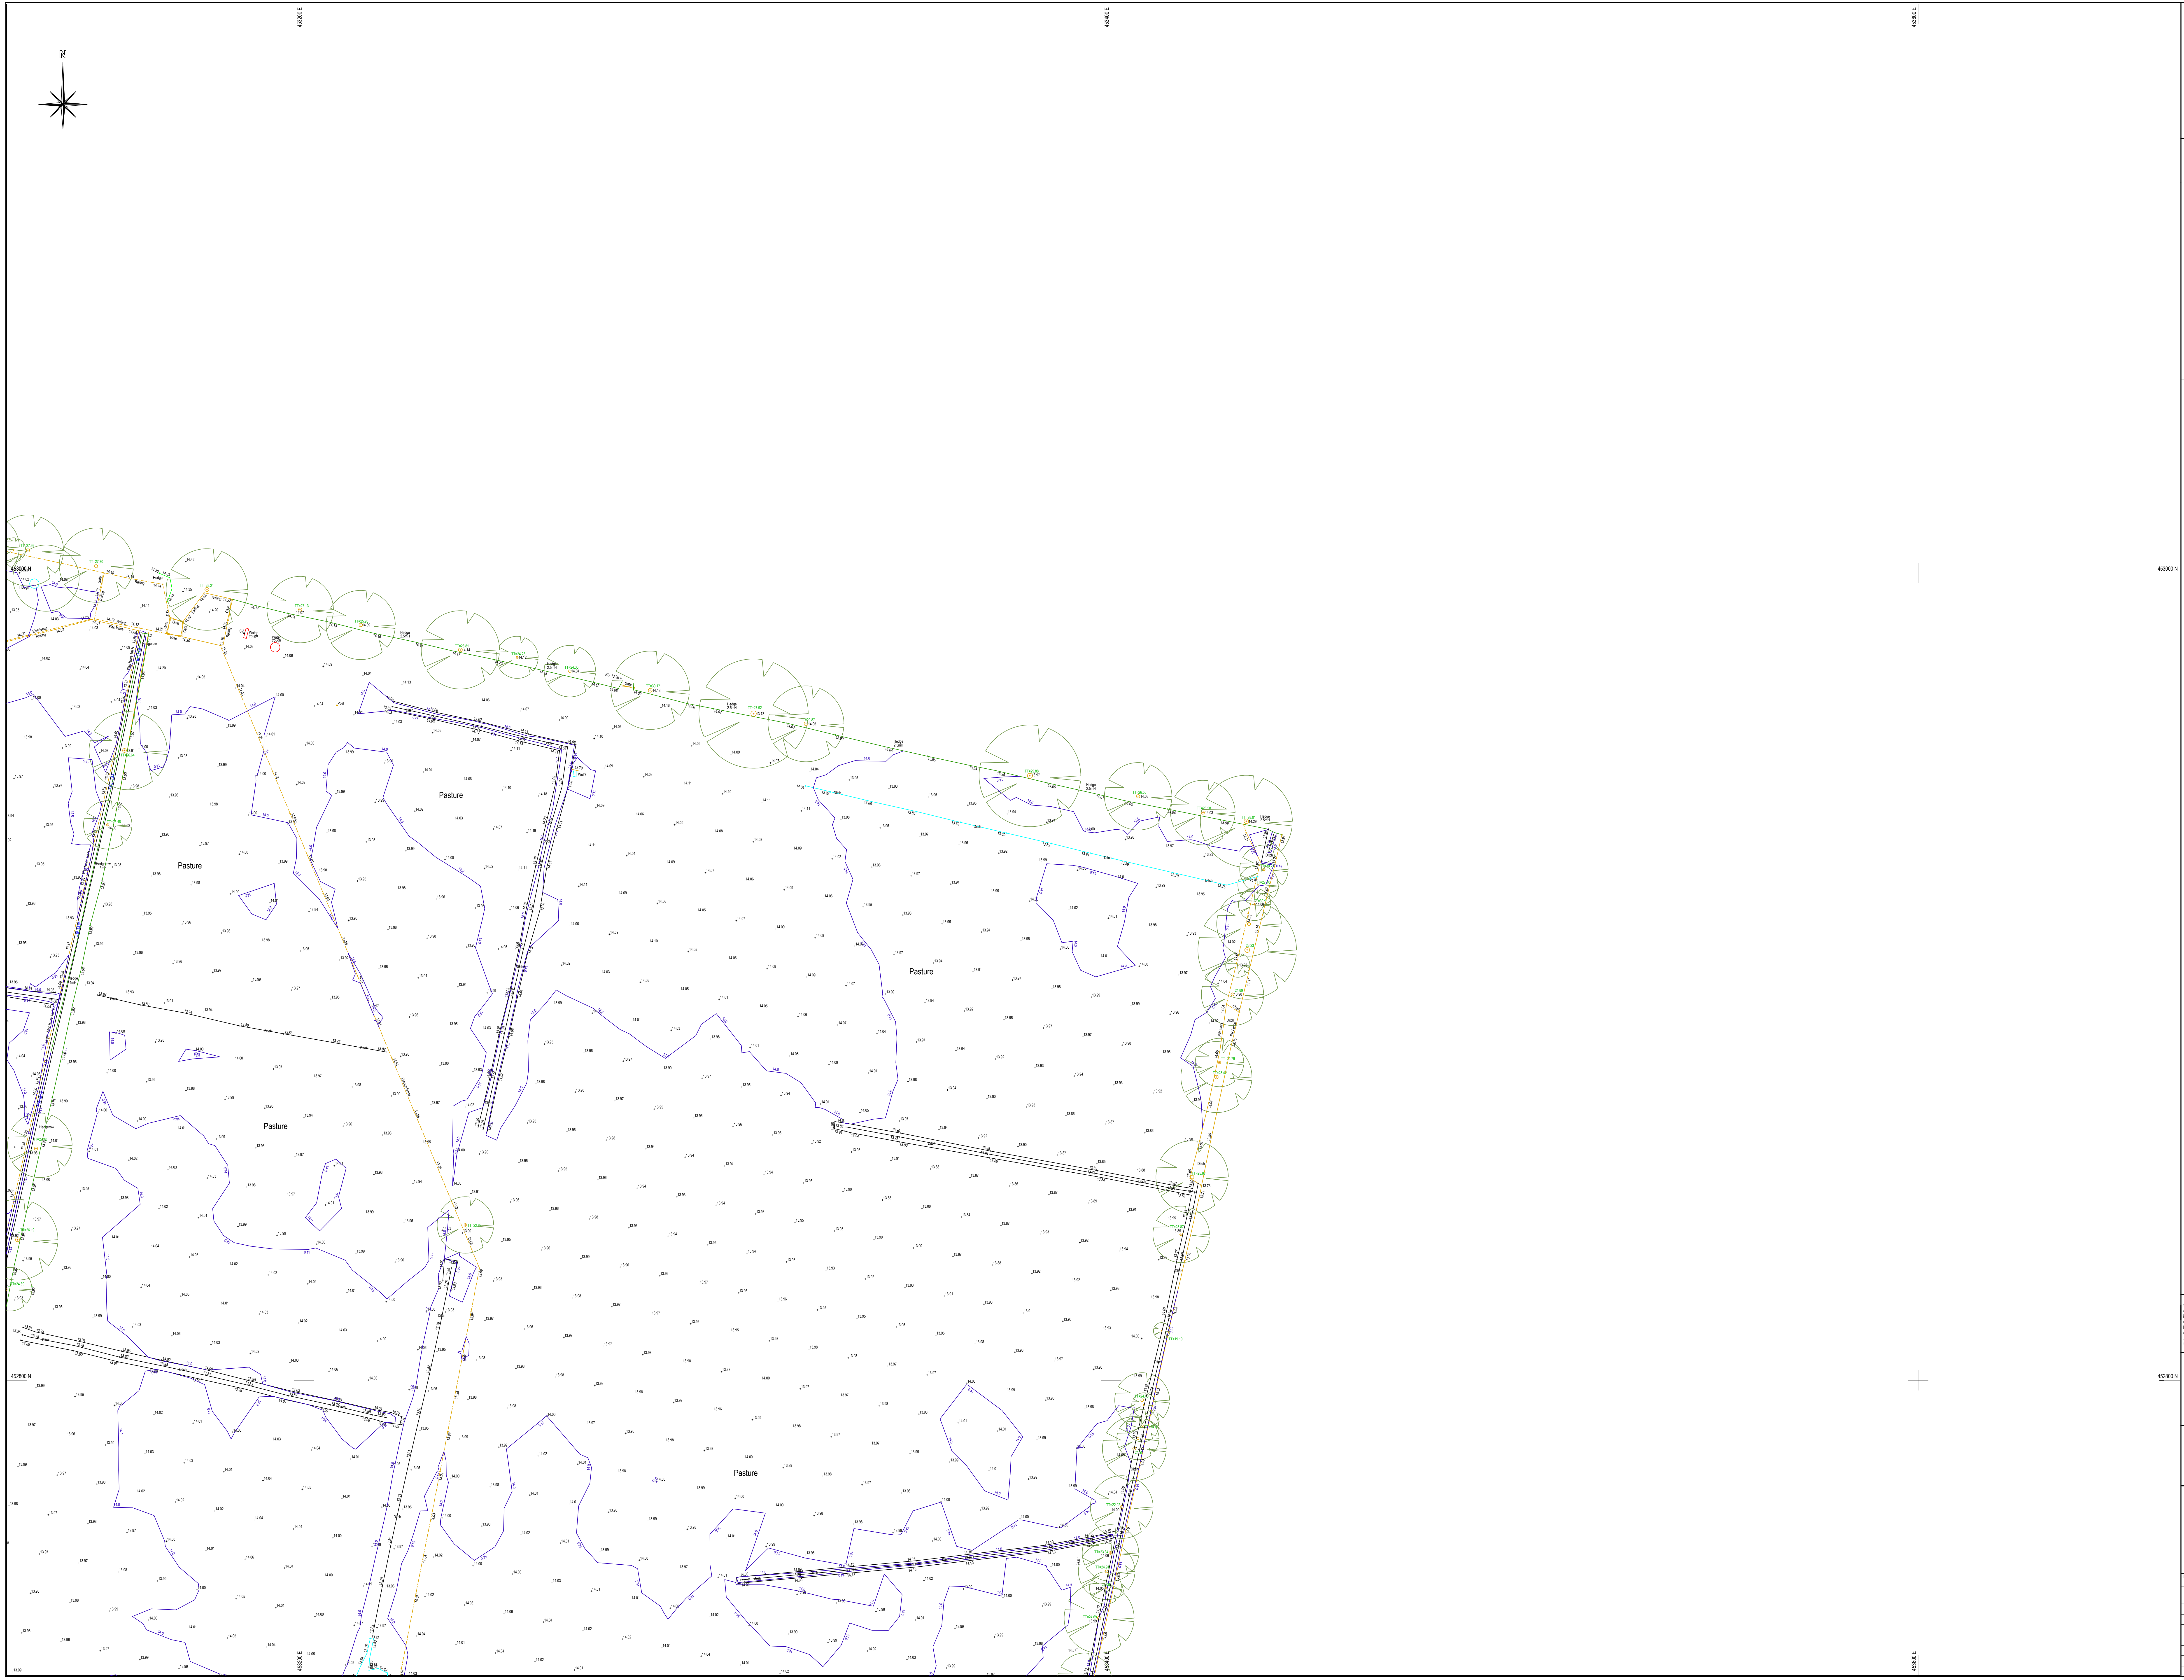
N
453200 E
453400 E
453600 E
453000 N
452800 N
Pasture
Pasture
Pasture
Pasture
Pasture
Pasture
Hedge
Hedge 2.5mH
Hedgerow
Hedgerow 3mH
Hedge 4mH
Railing
Gate
Elec fence
Elec fence 1m H
Electric fence
Water trough
Trough
SV
Post
Well?
Ditch
PW fence
PR Fence
BL=13.26
TT=27.99
TT=27.70
TT=25.21
TT=27.13
TT=25.95
TT=26.81
TT=24.23
TT=24.35
TT=30.17
TT=27.92
TT=29.87
TT=29.88
TT=26.58
TT=28.01
TT=26.64
TT=25.48
TT=27.48
TT=26.19
TT=24.39
TT=22.87
TT=30.91
TT=26.23
TT=24.89
TT=24.79
TT=23.42
TT=25.87
TT=23.87
TT=19.10
TT=22.02
TT=23.34
TT=24.91
TT=24.68
14.0

Topographical Survey Legend

B	Bollard	G	Gully	RS	Road sign	AL	Arch level
Bin	Litter bin	GP	Gate post	RW	Retaining Wall	BL	Bed level
BS	Bus stop	GV	Gas valve	SP	Soil pipe	CL	Cover level
BT	British telecom ic	IC	Inspection cover	ST	Stop tap	EL	Eaves level
CB	Control Box	JB	Junction box	Stay	Cable stay	FL	Floor level
CATV	Cable television cover	KO	Kerb outlet	SV	Stop valve	FT	Fence Top Level
CONC.	Concrete	LB	Letter box	TB	Traffic Bollard	H	General Height
DC	Drainage Channel	LP	Lamp post	TCB	Telephone call box	IL	Invert level
DK	Drop Kerb	Mkr	Utility marker	TL	Traffic light	PL	Parapet level
DP	Rain Water Downpipe	MH	Manhole	TP	Telegraph pole	RL	Roof/ridge level
DPM	Damp Proof Membrane	MP	Mile post	TPS	Tactile paving slabs	SL	Soffit level
EP	Elec. pole	NB	Notice Board	VP	Vent pipe	Spr	Arch springing level
ER	Earth rod	P	Post	WM	Water meter	Thr	Threshold level
FP	Flagpole	PM	Parking meter	WO	Water orifice	TT	Tree Top Level
FH	Fire Hydrant	RE	Rodding eye	UTL	Unable to lift	WL	Water level
		RS	Road sign	U/S	Underside of tree canopy (m)	WT	Top of Wall Level
						∅	Diameter

Level prefix descriptions

Fence annotation

B/W	Barbed wire
C/B	Closed boarded
C/I	Corrugated iron
C/L	Chain link
C/P	Concrete panel
H/R	Hand rail
I/R	Iron railings
O/B	Open boarded
P/C	Post & chain
P/R	Post & rail
P/W	Post & wire
W/M	Wire mesh

Details added using OS Ordnance Survey data

Fence

Gate

+ Stile

Hedge

50.00 + Spot level

+ STN6 Survey obs location

STN1 50.00 Survey control station (Coordinated point)

Tree

Bush

Levels defining edge of carriageway are observed at channel (bottom of kerb) unless otherwise stated.

Sheet Layout (Not to scale)


01
02
03
04
05
06
07

The accuracy of this survey is commensurate with the drawing scale specified within the title block. The drawing and all information contained therein is issued in confidence and remains the copyright of First Point Surveys Ltd. Disclosure of this information to Third Parties without permission is forbidden as is copying or replication.
Do not scale from this drawing, work to figured dimensions. Check all dimensions on-site. In the event of any discrepancy, please refer query to First Point Surveys Ltd.
Any boundaries shown are physical features on-site and do not necessarily represent the legal extents of ownership.

Levels related to Ordnance Survey Datum (OSGM15) using GPS

Coordinates related to Ordnance Survey grid (OSBG36) using GPS

This Topographical Survey has been produced using an orthographic coordinate grid, site centred around GCP 453335.017E, 452372.066N (as shown)

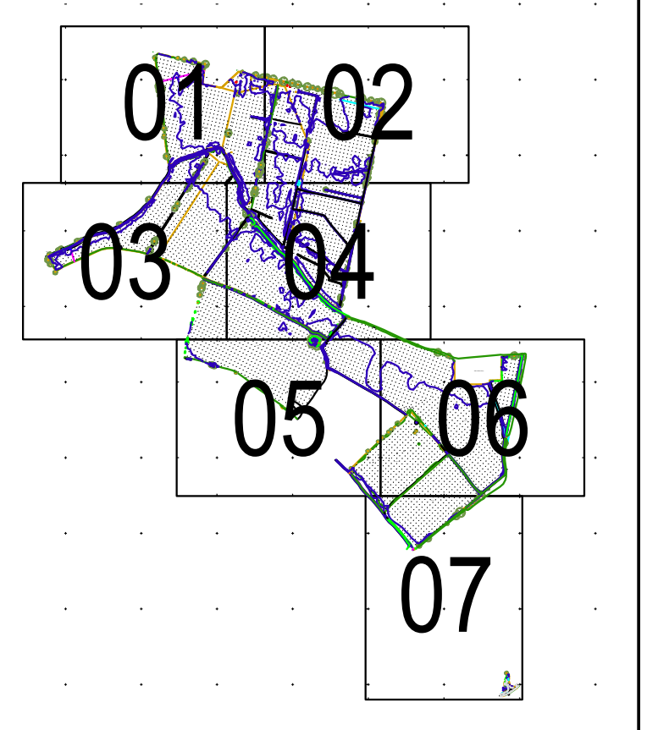Hedge heights are relative to adjacent field levels

Spot levels generated from a DTM surveyed at suitable spacings on site

Please note due to obstructions such as vegetation, First Point Surveys cannot guarantee all pertinent information has been surveyed.

FIRST POINT SURVEYS
Land, Building & Underground Utility Surveyors
2, Stoneacre ■ Grimbald Crag Close ■ Knaresborough ■ HG5 8PJ
Tel: 01423 869351 & 01423 883371
info@FirstPointSurveys.co.uk ■ www.FirstPointSurveys.co.uk

TITLE

Sheet 02
Topographical Survey
Rufforth Solar Farm
Rufforth / Hessay
York

DATE	DRAWN BY	CHKD. BY
March 2023	SRH / MIH	MIH

DRG NO	PLOT SCALE
7124 - 02	1: 500 @ A0

REV	AMENDMENT	DATE	BY	CHKD.