


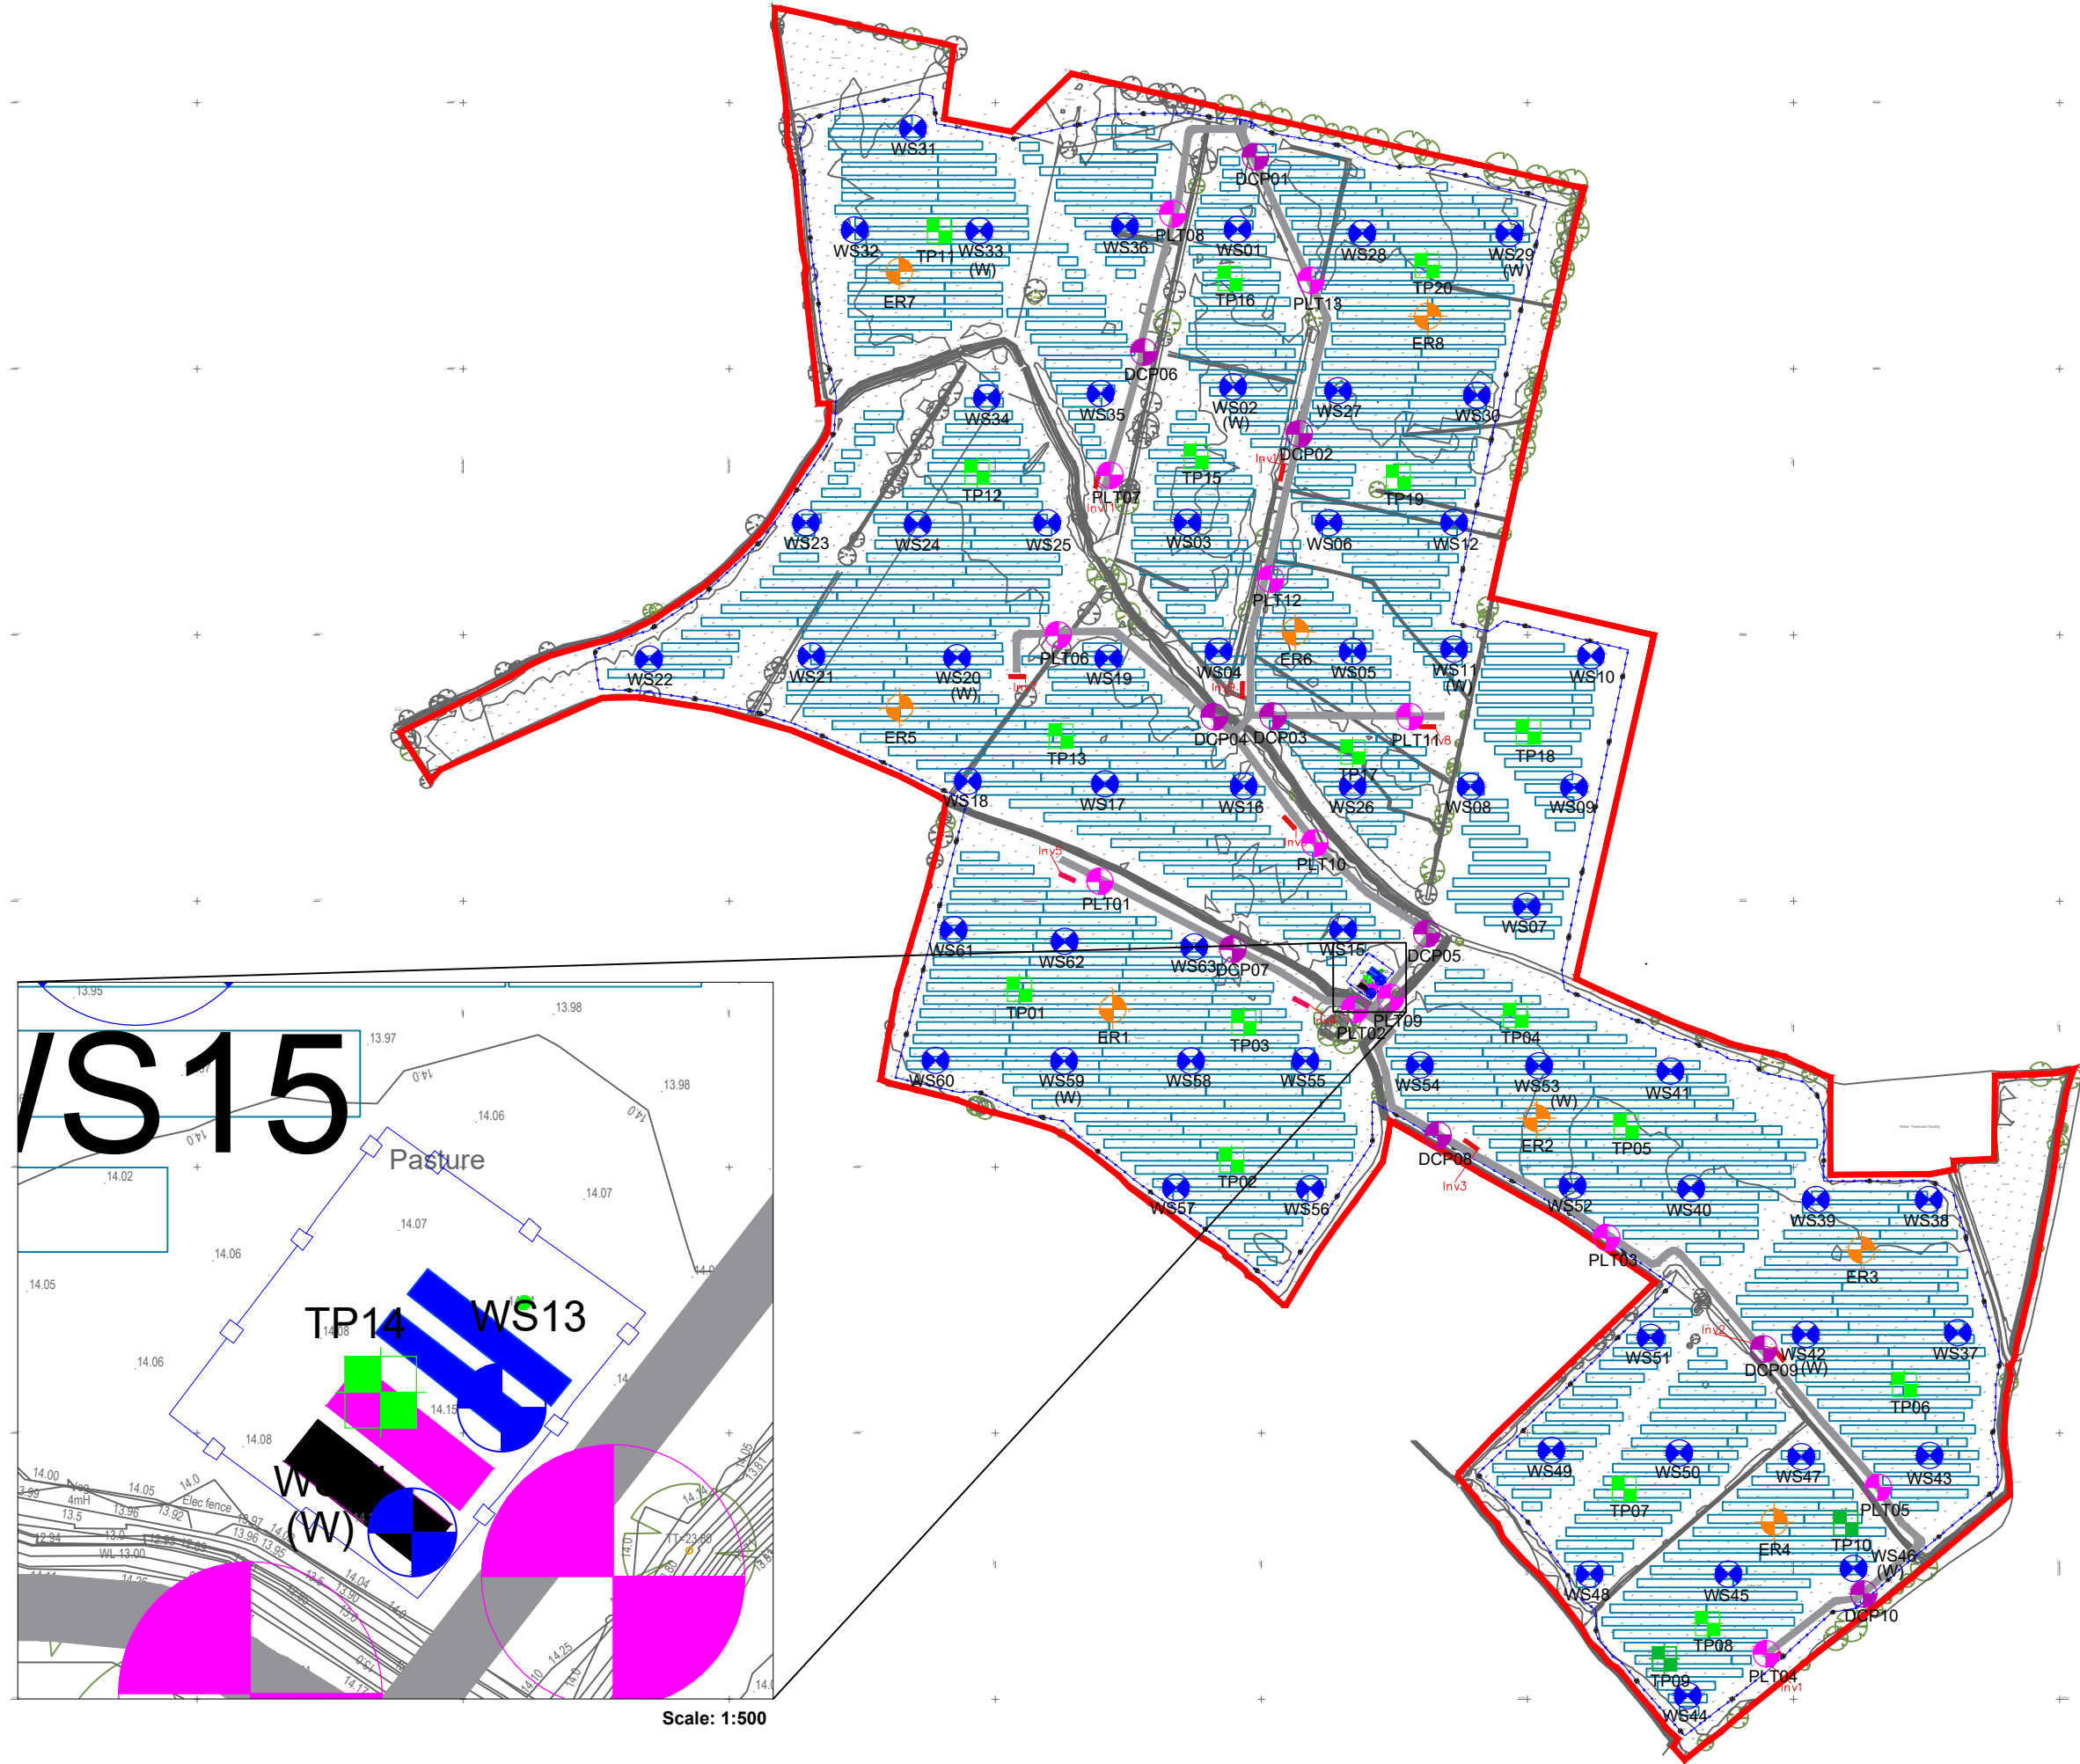

- NOTES**
- Site Boundary
 - Window Sample Borehole
 - (W) Groundwater Monitoring Install Locations
 - TRL Testing Location
 - Soil (electronic) Resistance Survey
 - Plate Load Testing Location
 - Trial Pit for General Ground Conditions
 - Trial Pit with Thermal Resistivity Testing

Notes

- This drawing should not be viewed in isolation from the accompanying report.
- All exploratory hole locations are based on survey grade GPS coordinates unless stated otherwise on the exploratory hole logs.
- The locations of services shown on this drawing are approximate and are based on utility plans provided by the client. Locations of services are given for the purposes of indicating constraints to the site investigation only. Reference should be made to original utility plans and HSG47 for locating of services within the site.
- All marked site features shown on this drawing are given for indicative purposes only. This drawing should not be underlaid in isolation to determine proposed development layouts. Reference should be made to the accompanying report for commentary on the potential location of these features including coordinates if available and any further works required to locate features if required.

REVISION		BY	DATE
0	Initial issue	JC	27/04/26
A	>>	>>	>>
B	>>	>>	>>
C	>>	>>	>>
D	>>	>>	>>

SIRIUS
GEOTECHNICAL LTD
4245 Park Approach,
Thorpe Park,
Leeds
LS15 8GB
www.thesiriusgroup.com
TEL: 0113 264 9960
FAX: 0113 264 9962



CLIENT

Hessay Solar Limited

SITE

**Hessay Solar Farm,
York**

DRAWING TITLE

**Exploratory Hole
Location Plan**

DRAWING NO. C10738/EHLP		REVISION NO. 0	
DRAWN BY JC		APPROVED BY AC	
DATE April 2026	SCALE 1:5000	PAPER SIZE A3	