
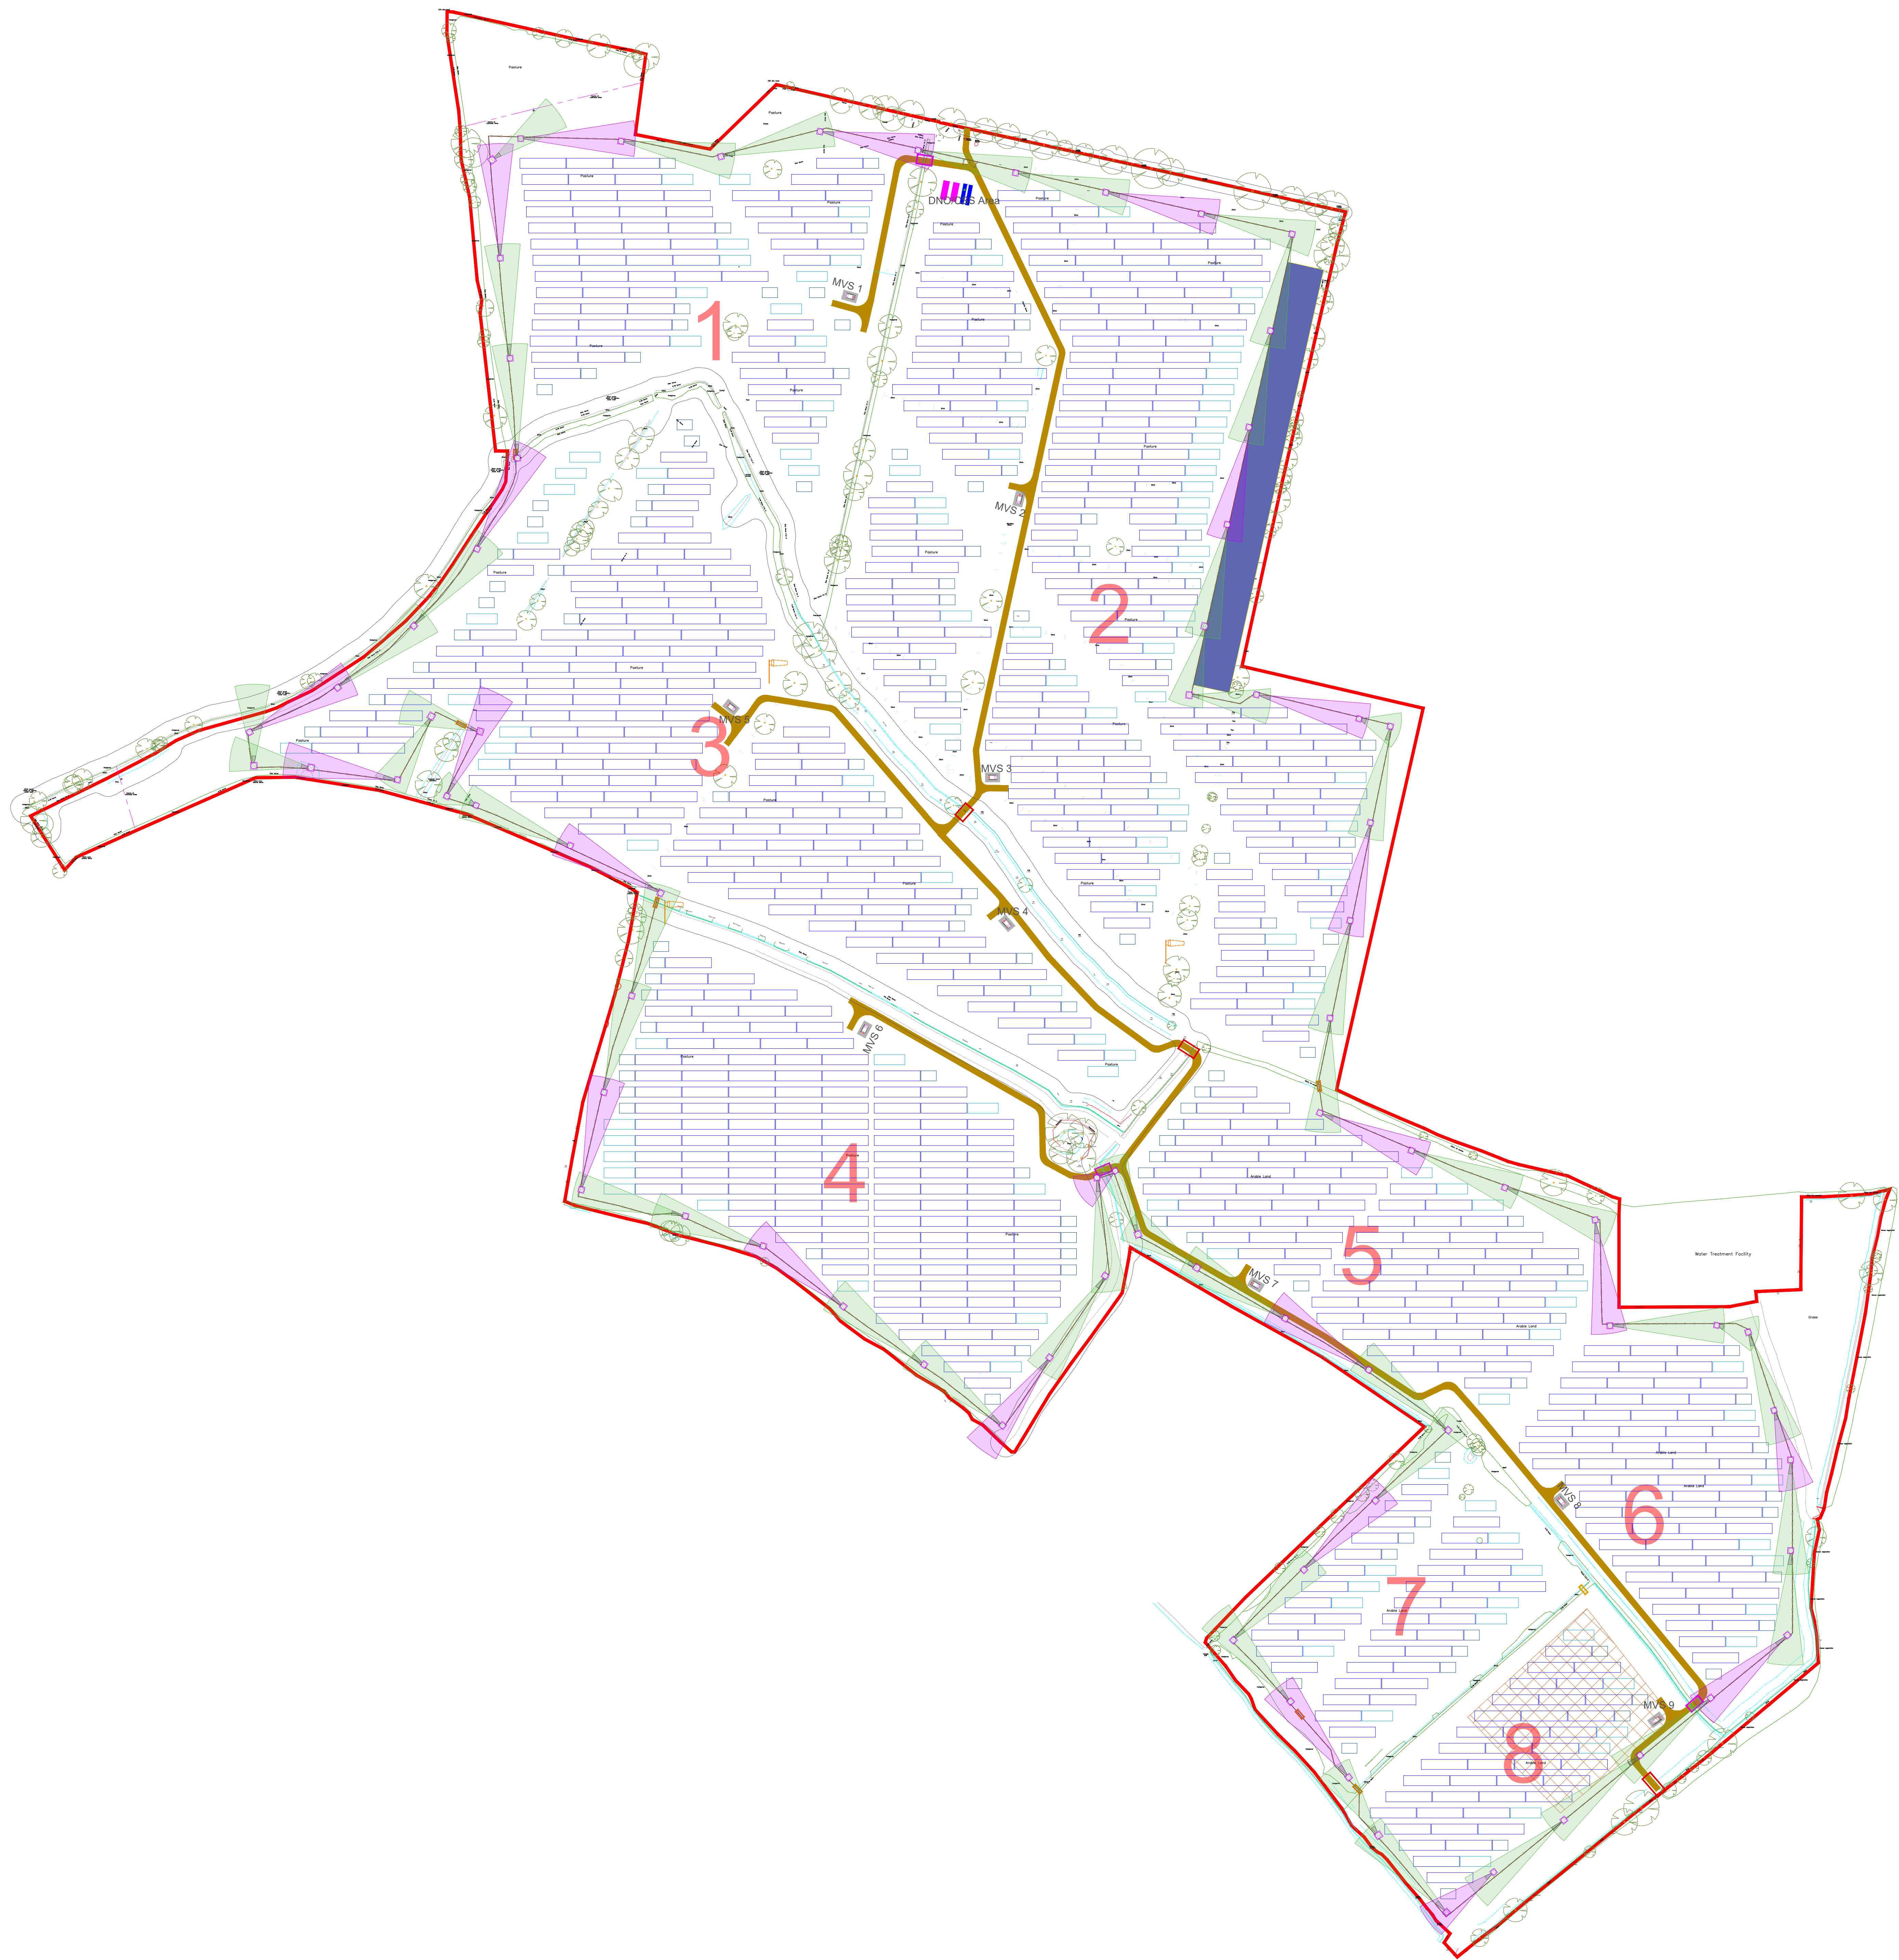


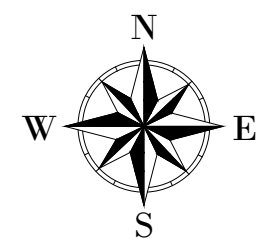

- NOTES**
1. THIS DRAWING TO BE READ IN CONJUNCTION WITH ALL RELEVANT ENGINEERS AND SPECIALISTS DRAWINGS & SPECIFICATIONS.
 2. ANY DISCREPANCIES BETWEEN THIS DRAWING AND ANY OTHER TO BE REPORTED TO THE ENGINEER IMMEDIATELY.
 3. ALL WORKS TO COMPLY WITH THE MOST CURRENT BRITISH STANDARDS.
 4. ALL DIMENSIONS IN MILLIMETERS UNLESS STATED OTHERWISE. NO DIMENSIONS ARE TO BE SCALED OFF THE DRAWING. USE FIGURED DIMENSIONS ONLY.
 5. ALL DIMENSIONS TO BE ±3mm UNLESS SPECIFIED OTHERWISE.

LEGEND

	Planning/Red Line Boundary
	Perimeter Fence
	Access Track
	PV Table - 3 x 9 Modules
	PV Table - 3 x 18 Modules
	PV Table - 3 x 27 Modules
	Temporary Construction Compound
	MVS (Smart Transformer Station-STs)
	Existing Trees
	Field Number
	Wind Sock
	6m Gate
	Top of Bank
	Bottom of Bank
	CSS/ DNO substation
	Spares Cabin
	25m Wide Landing Strip
	CCTV Master Camera
	CCTV Slave Camera
	Culvert Crossing - AT, Fence, CCTV and HV
	Culvert Crossing - AT and HV
	Ditch Crossing - CCTV and Fence
	Ditch Crossing - Cables & Ducts

Site Details:

	Model	Rating	Qty	Total Capacity
Modules	JAM60D45-640LB	640Wp	76815 (total)	49.16MWp
			2645 string	
Inverter	SG350HX	352kVA	125	44MVA
		3520kVA	3	
TX Station	MV/S4490	4928kVA	3	46.46MVA
	MV/S6400	7040kVA	3	
Tilt & Pitch		16°, 10.945m		
Nominal Voltage at Connection Point		33kV ICP		
Export Capacity		40MW @0.95 PF		
Import Capacity		335 kVA		

0	First Issued			
	GF	KN	AH	17/04/2026
REV	DESCRIPTION			
	DESIGNED	CHECKED	APPROVED	DATE



ETHICAL POWER LTD.
UNIT 9, DUNCHIEOCK BARTON,
DUNCHIEOCK, SKETER
EX2 9JL
(0) 17726 218618
www.ethical-power.com

Project: EC006 - HESSAY

Title: CCTV Layout

Drawing Status: PRELIMINARY

Grid Ref (8 fig):
Site address: LOW MOOR LANE,
YORK,
YO26 8JT

DWG No.	SHEET	SCALE (A0)	REV.
EP-EC006-CCTV-1	1 OF 1	1:1750	00