
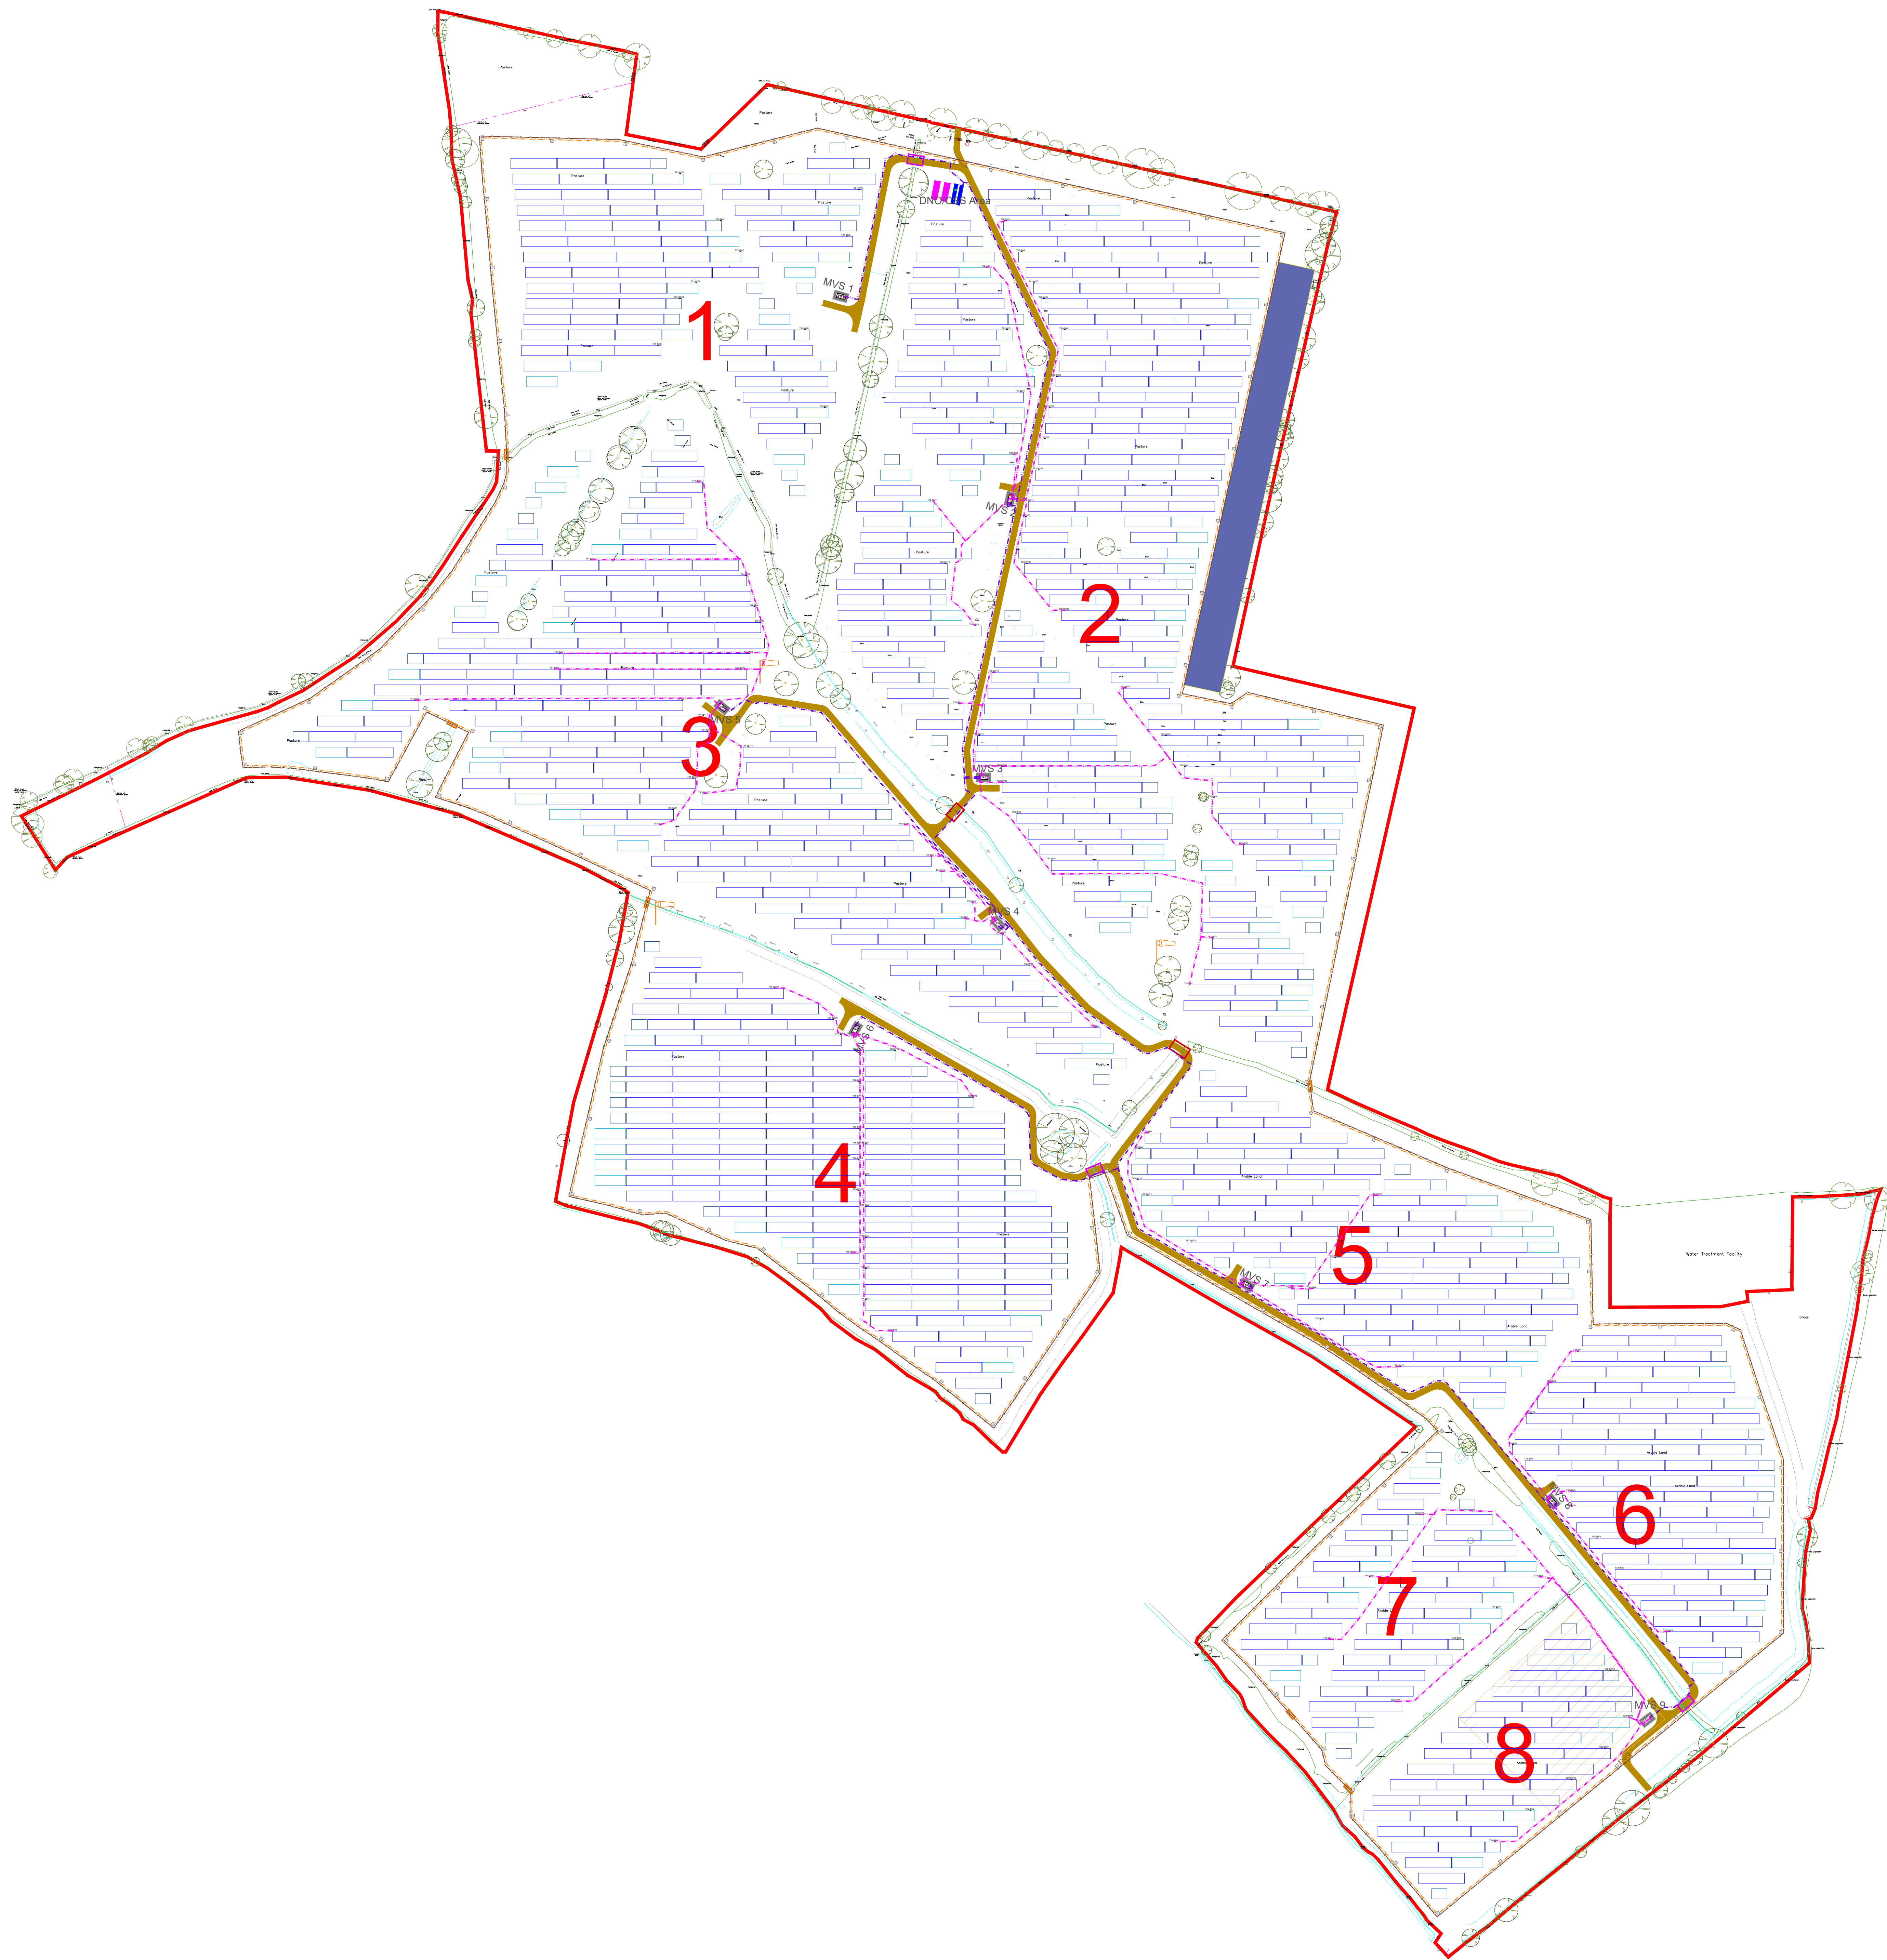


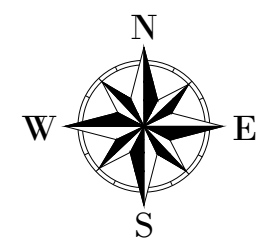

- NOTES**
1. THIS DRAWING TO BE READ IN CONJUNCTION WITH ALL RELEVANT ENGINEERS AND SPECIALISTS DRAWINGS & SPECIFICATIONS.
 2. ANY DISCREPANCIES BETWEEN THIS DRAWING AND ANY OTHER TO BE REPORTED TO THE ENGINEER IMMEDIATELY.
 3. ALL WORKS TO COMPLY WITH THE MOST CURRENT BRITISH STANDARDS.
 4. ALL DIMENSIONS IN MILLIMETERS UNLESS STATED OTHERWISE. NO DIMENSIONS ARE TO BE SCALED OFF THE DRAWING. USE FIGURED DIMENSIONS ONLY.
 5. ALL DIMENSIONS TO BE ±3mm UNLESS SPECIFIED OTHERWISE.

LEGEND

	Planning/Red Line Boundary
	Perimeter Fence
	Access Track
	PV Table - 3 x 9 Modules
	PV Table - 3 x 18 Modules
	PV Table - 3 x 27 Modules
	Temporary Construction Compound
	MVS (Smart Transformer Station-STs)
	Existing Trees
	Field Number
	Wind Sock
	6m Gate
	Top of Bank
	Bottom of Bank
	CSS/ DNO substation
	Spares Cabin
	25m Wide Landing Strip
	CCTV Location
	Culvert Crossing - AT , Fence, CCTV and HV
	Culvert Crossing - AT and HV
	Ditch Crossing - CCTV and Fence
	HV Trench - 1 Circuit
	HV Trench - 2 Circuit
	LV Trench
	CCTV Trench

0	Preliminary Issue			
	PM	AH	AH	24/03/2026
REV	DESCRIPTION			
	DESIGNED	CHECKED	APPROVED	DATE



ETHICAL POWER LTD.
UNIT 9, DUNCHIDECK BARTON,
DUNCHIDECK, SKIPTON
YO2 9JL
(01728) 218618
www.ethical-power.com

Project: EC006 - HESSAY

Title: TCH OVERVIEW

Drawing Status: PRELIMINARY

Grid Ref (if in):
Site Ref (if in): LOW MOOR LANE,
DUNCHIDECK, SKIPTON
YO2 9JL

DWG No:	SHEET	SCALE (A0)	REV.
EP-EC006-TCH-1	1 OF 1	1:1750	00