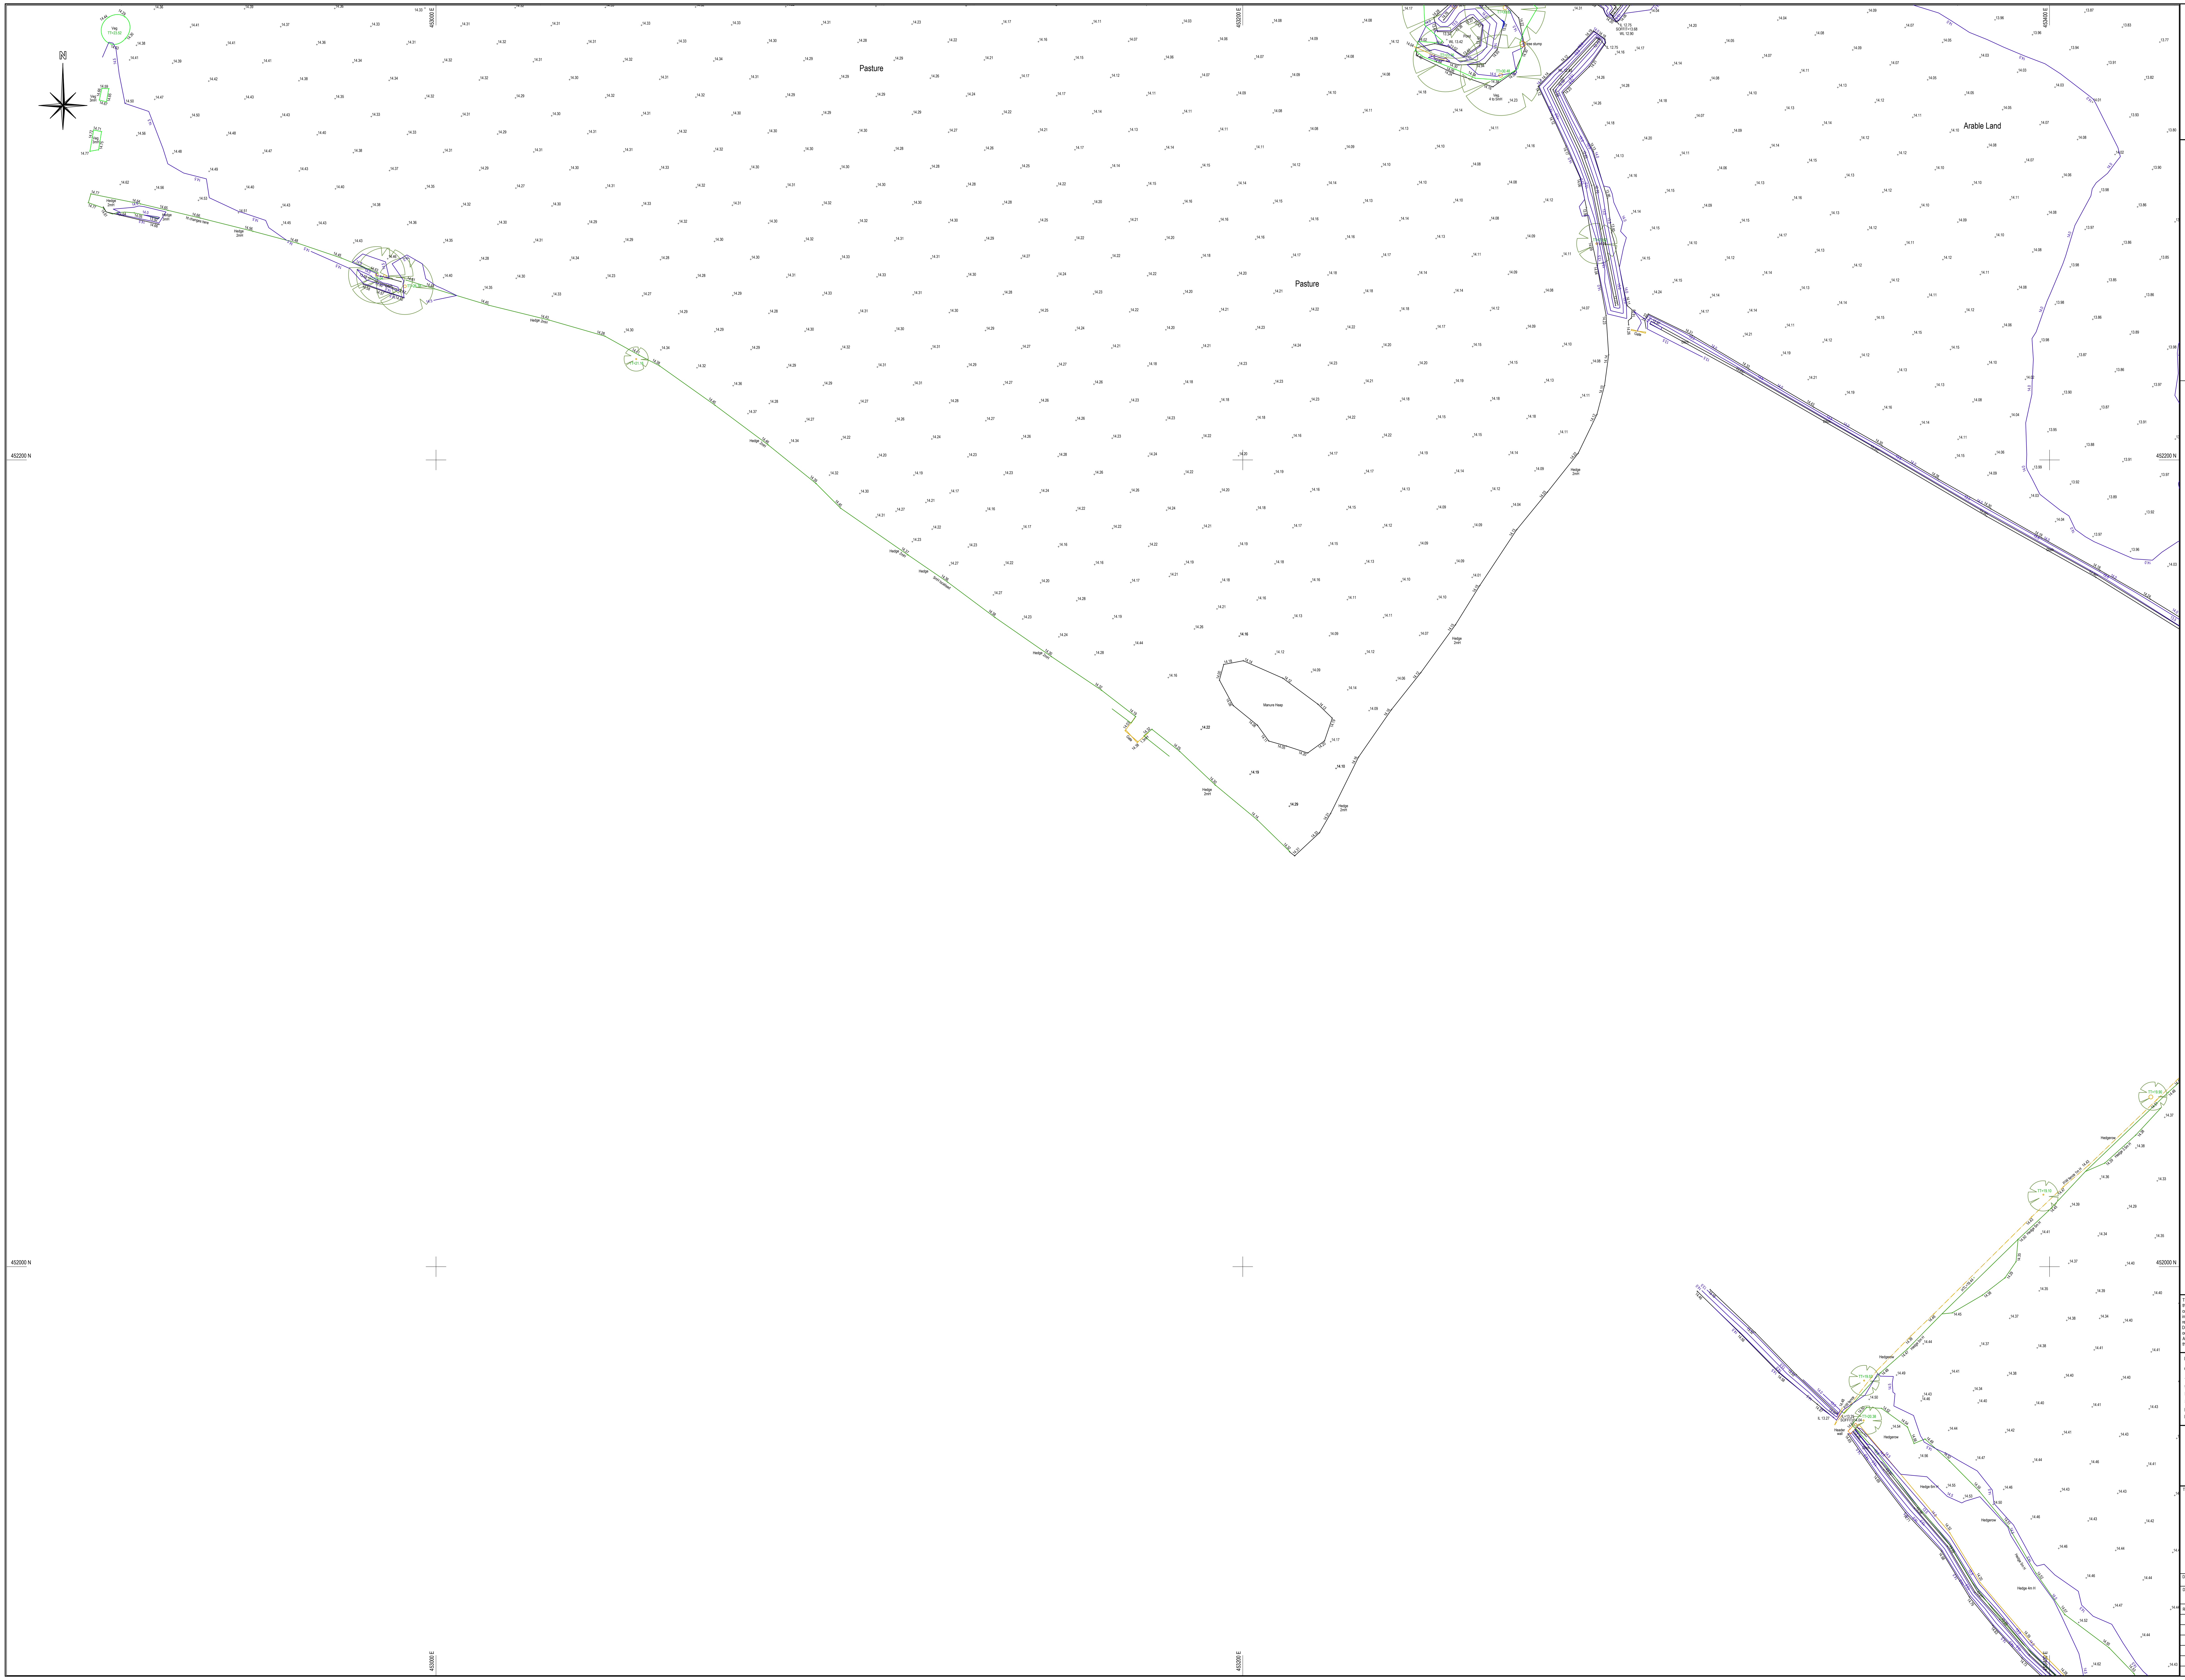

Topographical Survey Legend

B	Bollard
Bin	Litter bin
BS	Bus stop
BT	British telecom ic
CB	Control Box
CATV	Cable television cover
CONC.	Concrete
DC	Drainage Channel
DK	Drop Kerb
DP	Rain Water Downpipe
DPM	Damp Proof Membrane
EP	Elec. pole
ER	Earth rod
FP	Flagpole
FH	Fire Hydrant
G	Gully
GP	Gate post
GV	Gas valve
IC	Inspection cover
JB	Junction box
KO	Kerb outlet
LB	Letter box
LP	Lamp post
Mkr	Utility marker
MH	Manhole
MP	Mile post
NB	Notice Board
P	Post
PM	Parking meter
RE	Rodding eye
RS	Road sign
RS	Road sign
RW	Retaining Wall
SP	Soil pipe
ST	Stop tap
Stay	Cable stay
SV	Stop valve
TB	Traffic Bollard
TCB	Telephone call box
TL	Traffic light
TP	Telegraph pole
TPS	Tactile paving slabs
VP	Vent pipe
WM	Water meter
WO	Water orifice
UTL	Unable to lift
U/S	Underside of tree canopy (m)

Level prefix descriptions

AL	Arch level
BL	Bed level
CL	Cover level
EL	Eaves level
FL	Floor level
FT	Fence Top Level
H	General Height
IL	Invert level
PL	Parapet level
RL	Roof/ridge level
SL	Soffit level
Spr	Arch springing level
Thr	Threshold level
TT	Tree Top Level
WL	Water level
WT	Top of Wall Level
∅	Diameter

Fence annotation

B/W	Barbed wire
C/B	Closed boarded
C/I	Corrugated iron
C/L	Chain link
C/P	Concrete panel
H/R	Hand rail
I/R	Iron railings
O/B	Open boarded
P/C	Post & chain
P/R	Post & rail
P/W	Post & wire
W/M	Wire mesh

Details added using OS Ordnance Survey data

Fence

Gate

Stile

Hedge

50.00 Spot level

STN6 Survey obs location

STN1 50.00 Survey control station (Coordinated point)

Tree

Bush

Levels defining edge of carriageway are observed at channel (bottom of kerb) unless otherwise stated.

Sheet Layout (Not to scale)

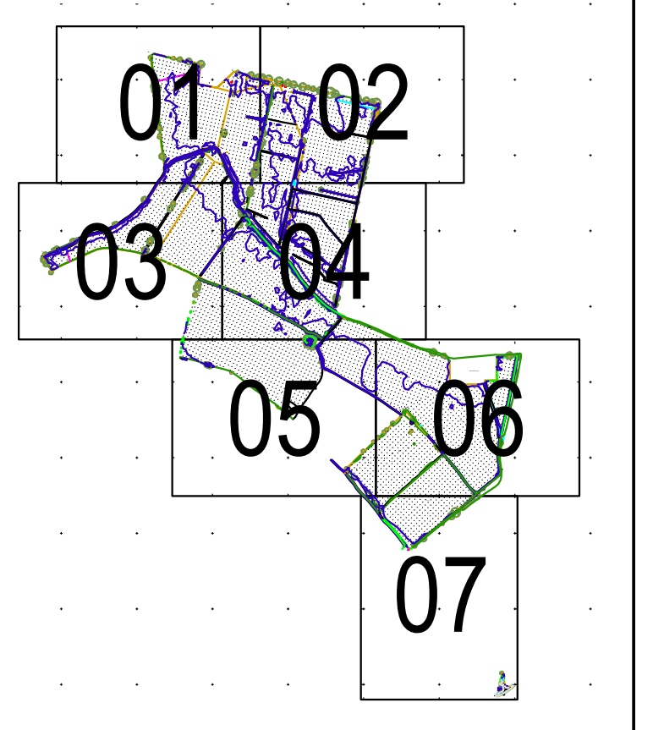

The accuracy of this survey is commensurate with the drawing scale specified within the title block. The drawing and all information contained therein is issued in confidence and remains the copyright of First Point Surveys Ltd. Disclosure of this information to Third Parties without permission is forbidden as is copying or replication.

Do not scale from this drawing, work to figured dimensions. Check all dimensions on-site. In the event of any discrepancy, please refer query to First Point Surveys Ltd. Any boundaries shown are physical features on-site and do not necessarily represent the legal extents of ownership.

Levels related to Ordnance Survey Datum (OSGM15) using GPS

Coordinates related to Ordnance Survey grid (OSBG36) using GPS

This Topographical Survey has been produced using an orthographic coordinate grid, site centred around GCP 453335.017E, 452372.066N (as shown)

Hedge heights are relative to adjacent field levels

Spot levels generated from a DTM surveyed at suitable spacings on site

Please note due to obstructions such as vegetation, First Point Surveys cannot guarantee all pertinent information has been surveyed.

FIRST POINT SURVEYS
LAND, BUILDING & UNDERGROUND UTILITY SURVEYORS
2, STONEACRE ▪ GRIMBALD CRAG CLOSE ▪ KNARESBOROUGH ▪ HG5 8PJ
TEL: 01423 869351 & 01423 883371
INFO@FIRSTPOINTSURVEYS.CO.UK ▪ WWW.FIRSTPOINTSURVEYS.CO.UK

TITLE

Sheet 05
Topographical Survey
Rufforth Solar Farm
Rufforth / Hessay
York

DATE	March 2023	DRAWN BY	SRH / MIH	CHKD. BY	MIH
DRG NO	7124 - 05	PLOT SCALE	1: 500 @ A0		

REV	AMENDMENT	DATE	BY	CHKD.