


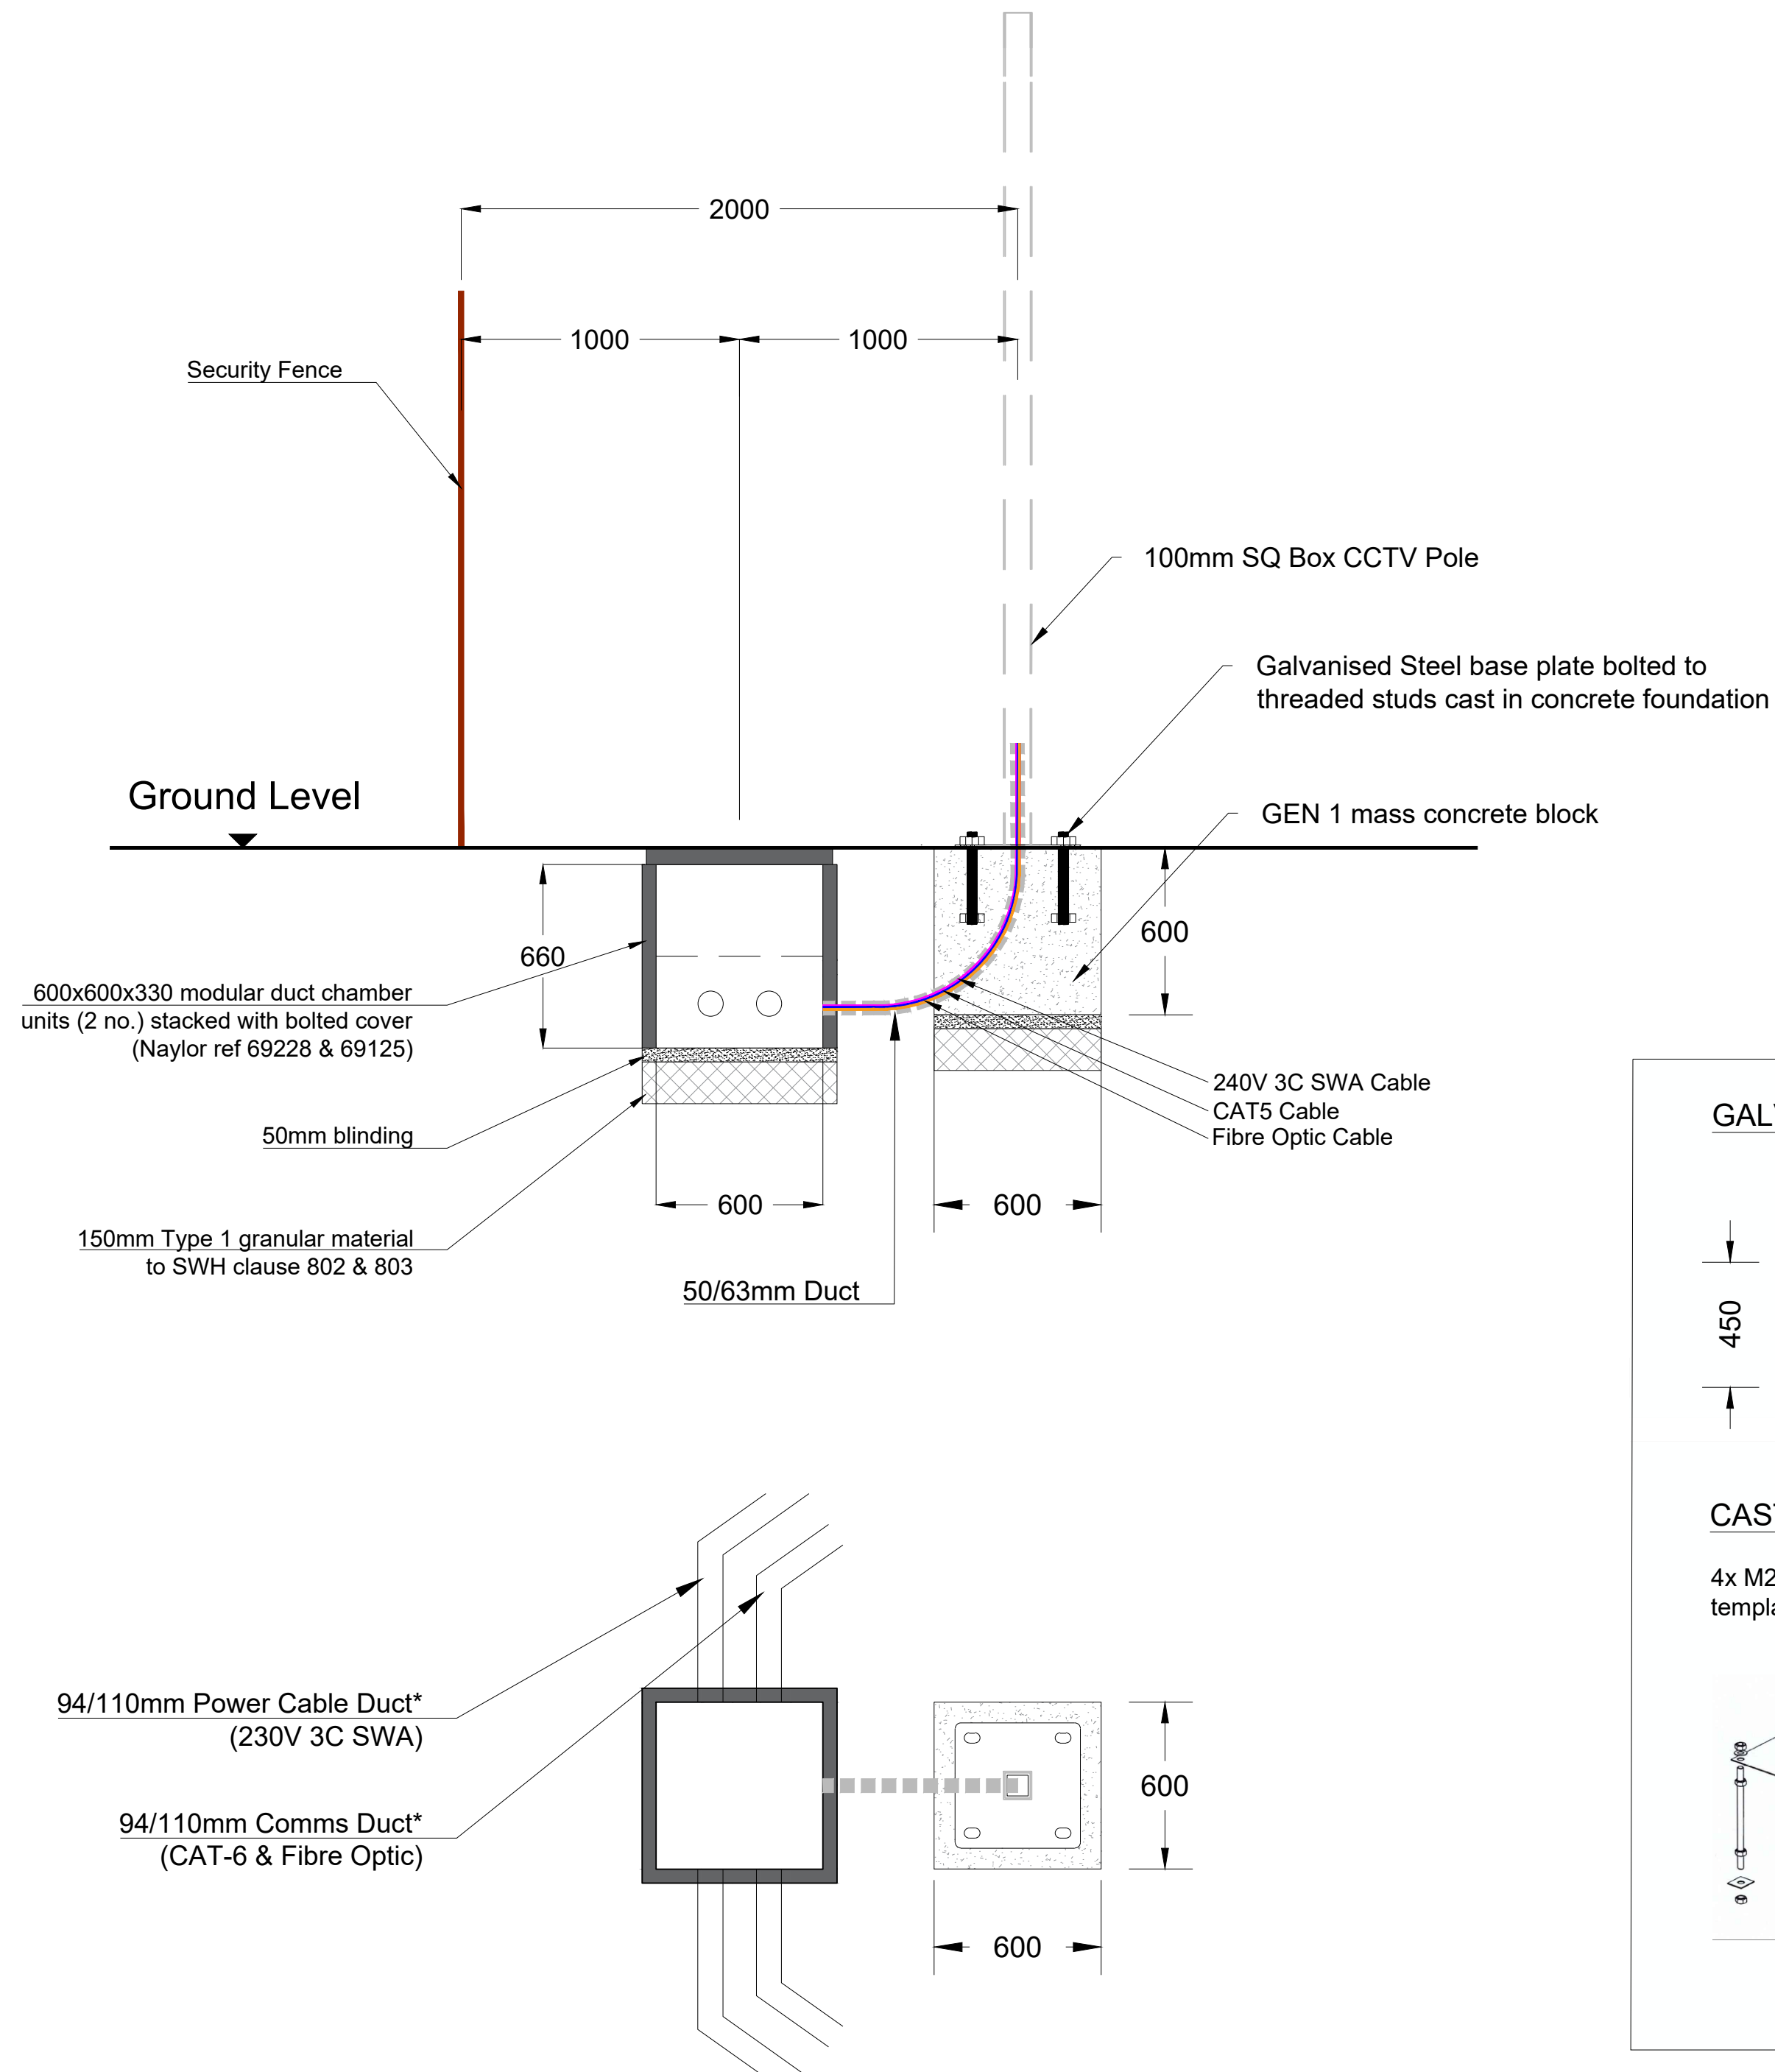

This document is protected by copyright and design rights. Any unauthorised reproduction, distribution, or use constitutes an infringement and may result in legal action.
©Ethical Power Ltd. All rights reserved.

NOTES

1. THIS DRAWING TO BE READ IN CONJUNCTION WITH ALL RELEVANT ENGINEERS AND SPECIALISTS DRAWINGS & SPECIFICATIONS.
2. ANY DISCREPANCIES BETWEEN THIS DRAWING AND ANY OTHER TO BE REPORTED TO THE ENGINEER IMMEDIATELY.
3. ALL WORKS TO COMPLY WITH THE MOST CURRENT BRITISH STANDARDS.
4. ALL DIMENSIONS IN MILLIMETERS UNLESS STATED OTHERWISE. NO DIMENSIONS ARE TO BE SCALED OFF THE DRAWING. USE FIGURED DIMENSIONS ONLY.
5. ALL DIMENSIONS TO BE $\pm 3\text{mm}$ UNLESS SPECIFIED OTHERWISE.

SCALE AT 1:20



Notes:

*Cable ducts to have 600mm cover, laid in sand with 100mm of cover and warning tape.

00	PRELIMINARY ISSUE			
	AE	KN	AK	06/05/2026

REV	DESCRIPTION			
	DESIGNED	CHECKED	APPROVED	DATE



ETHICAL POWER LTD,
UNIT 9, DUNCHIDEOCK BARTON,
DUNCHIDEOCK, EXETER
EX2 9UA
(t) 01726 218618
www.ethical-power.com

Project:

EC006 - HESSAY

Title:

SECURITY CAMERA ELEVATION

Drawing Status:

PRELIMINARY

Grid Ref (6 fig):

Site address: LOW MOOR LANE,
YORK,
YO268JT

DWG No:	SHEET:	SCALE (A2):	REV:
EP-EC006-ELV-SC-1	1 OF 1	1:20	00