


Option-1
Concrete Foundation

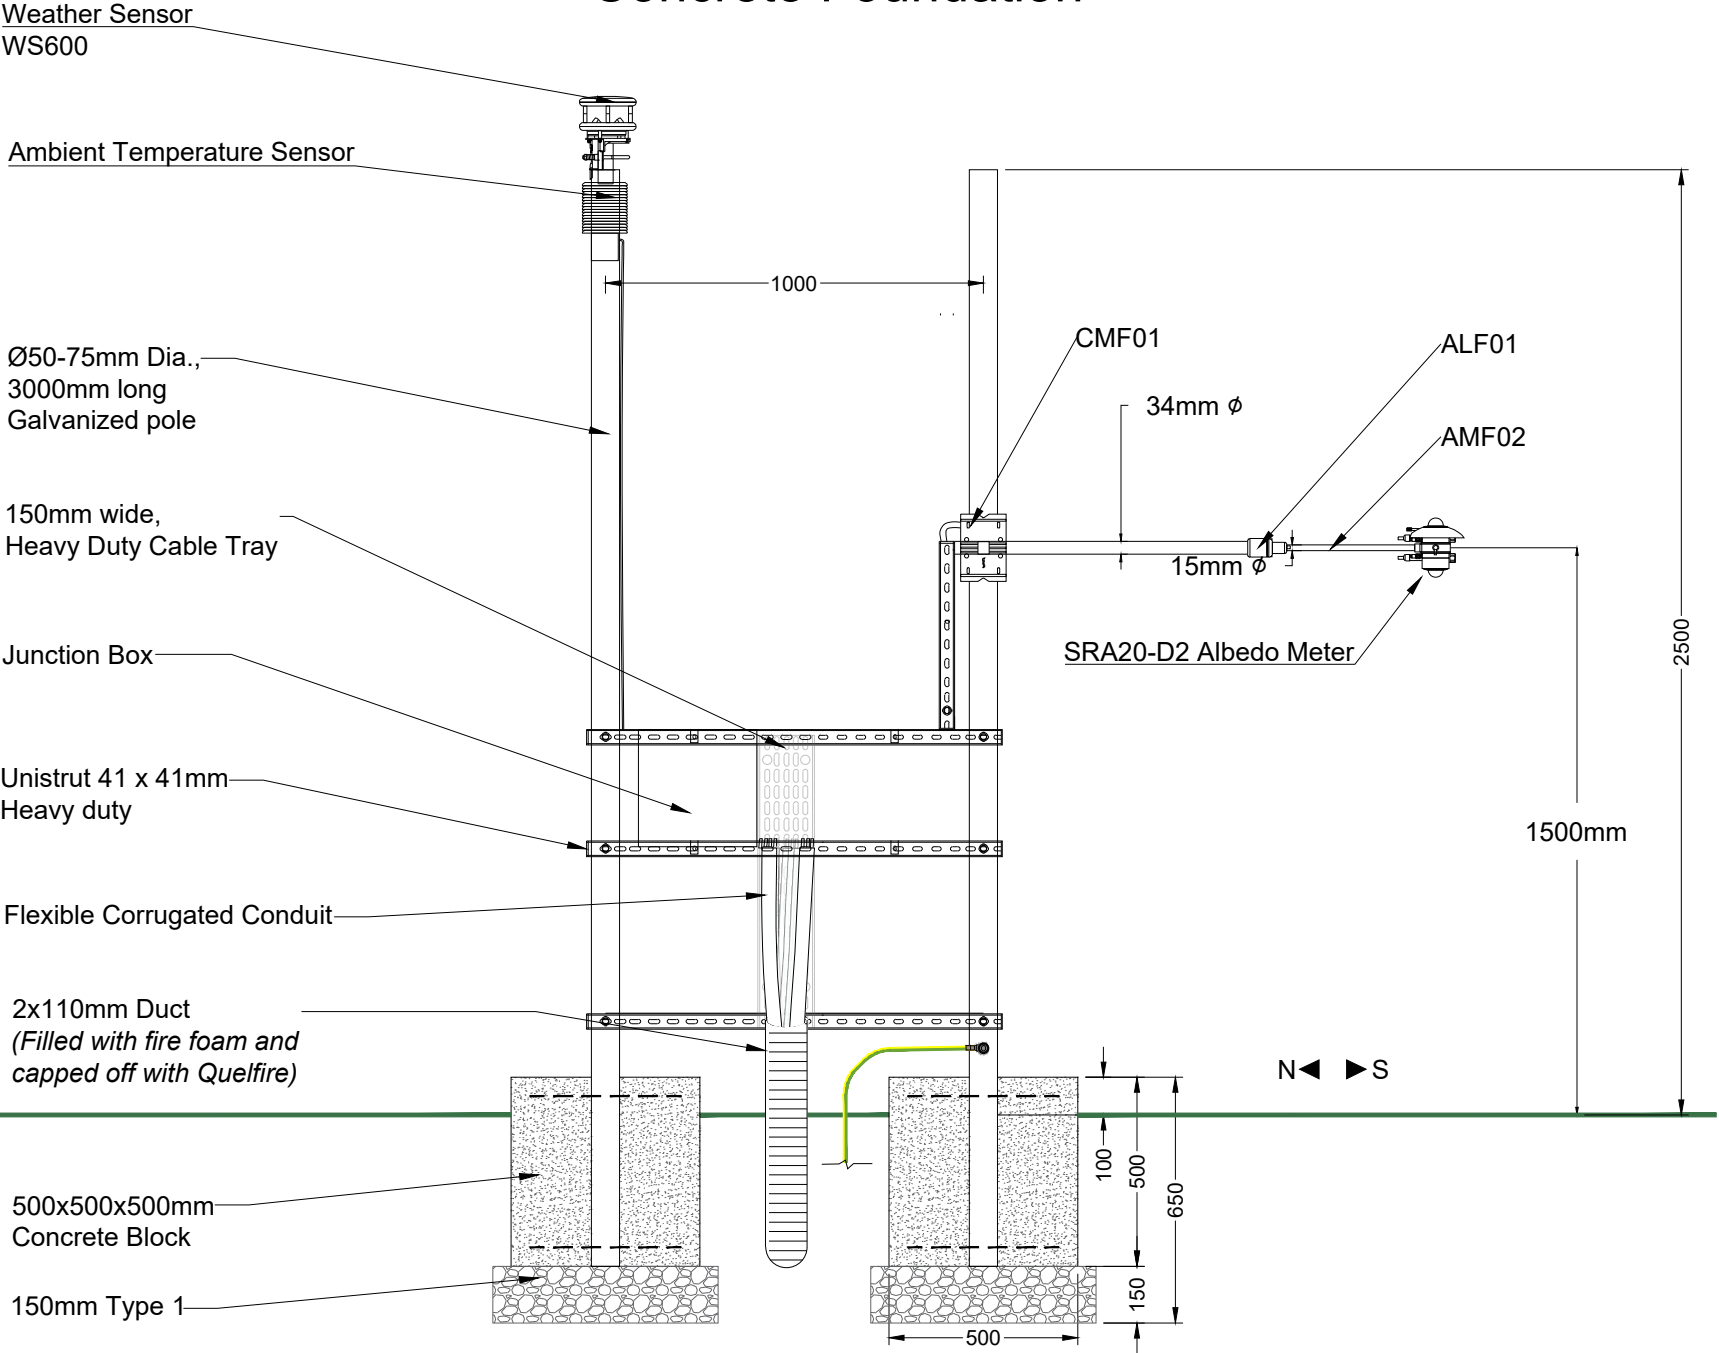

- Concrete Block Specification:
- Concrete: C25/30 to BS EN 206 / BS 8500
 - Exposure Class: XC2
 - Reinforcement: A393 mesh placed at top and bottom of block with 50mm minimum cover. No lap required as mesh is to be used in single continuous sheets cut to fit.
 - Support: Mesh to be set on 50mm concrete spacers
 - Foundation Material: Place block on 150mm well-compacted MOT Type 1 (min. 100kN/m² bearing capacity)
 - Tolerances: ±10mm level, ±20mm position
 - Construction Note: Ensure reinforcement is clean, tied, and positioned with adequate cover on all sides before pouring concrete. Cure concrete in accordance with BS EN 13670.

This document is protected by copyright and design rights. Any unauthorised reproduction, distribution, or use constitutes an infringement and may result in legal action.
©Ethical Power Ltd. All rights reserved.

Do not scale from this drawing

NOTES

- THIS DRAWING TO BE READ IN CONJUNCTION WITH ALL RELEVANT ENGINEERS AND SPECIALISTS DRAWINGS & SPECIFICATIONS.
- ANY DISCREPANCIES BETWEEN THIS DRAWING AND ANY OTHER TO BE REPORTED TO THE ENGINEER IMMEDIATELY.
- ALL WORKS TO COMPLY WITH THE MOST CURRENT BRITISH STANDARDS.
- ALL DIMENSIONS IN MILLIMETERS UNLESS STATED OTHERWISE. NO DIMENSIONS ARE TO BE SCALED OFF THE DRAWING. USE FIGURED DIMENSIONS ONLY.
- ALL DIMENSIONS TO BE ±3mm UNLESS SPECIFIED OTHERWISE.

16 Sqmm Soft Drawn Cu, insulated earth cable

50 Sqmm Soft Drawn Cu, insulated earth cable tapped from main earth Bolted to structure

Notes:
Refer to plots "EP-EC006-SEN-2" to "EP-EC006-SEN-3" for the sensor locations on the PV Park.
Refer to plot "EP-EC006-COMMS-1" for the indicative communications block diagram for the PV Park

00	PRELIMINARY ISSUE			
	AE	KN	AH	10/04/2026
REV	DESCRIPTION			
	DESIGNED	CHECKED	APPROVED	DATE



ETHICAL POWER LTD,
UNIT 9, DUNCHIDEOCK BARTON,
DUNCHIDEOCK, EXETER
EX2 9UA
(t) 01726 218618
www.ethical-power.com

Project: EC006 - HESSAY

Title: PYRO & ALBEDOMETER
ELEVATION

Drawing Status: PRELIMINARY

Grid Ref (6 fig):
Site address: LOW MOOR LANE,
YORK,
YO268JT

DWG No:	SHEET:	SCALE (A3):	REV:
EP-EC006-ELV-SEN-1	1 OF 1	NTS	00