


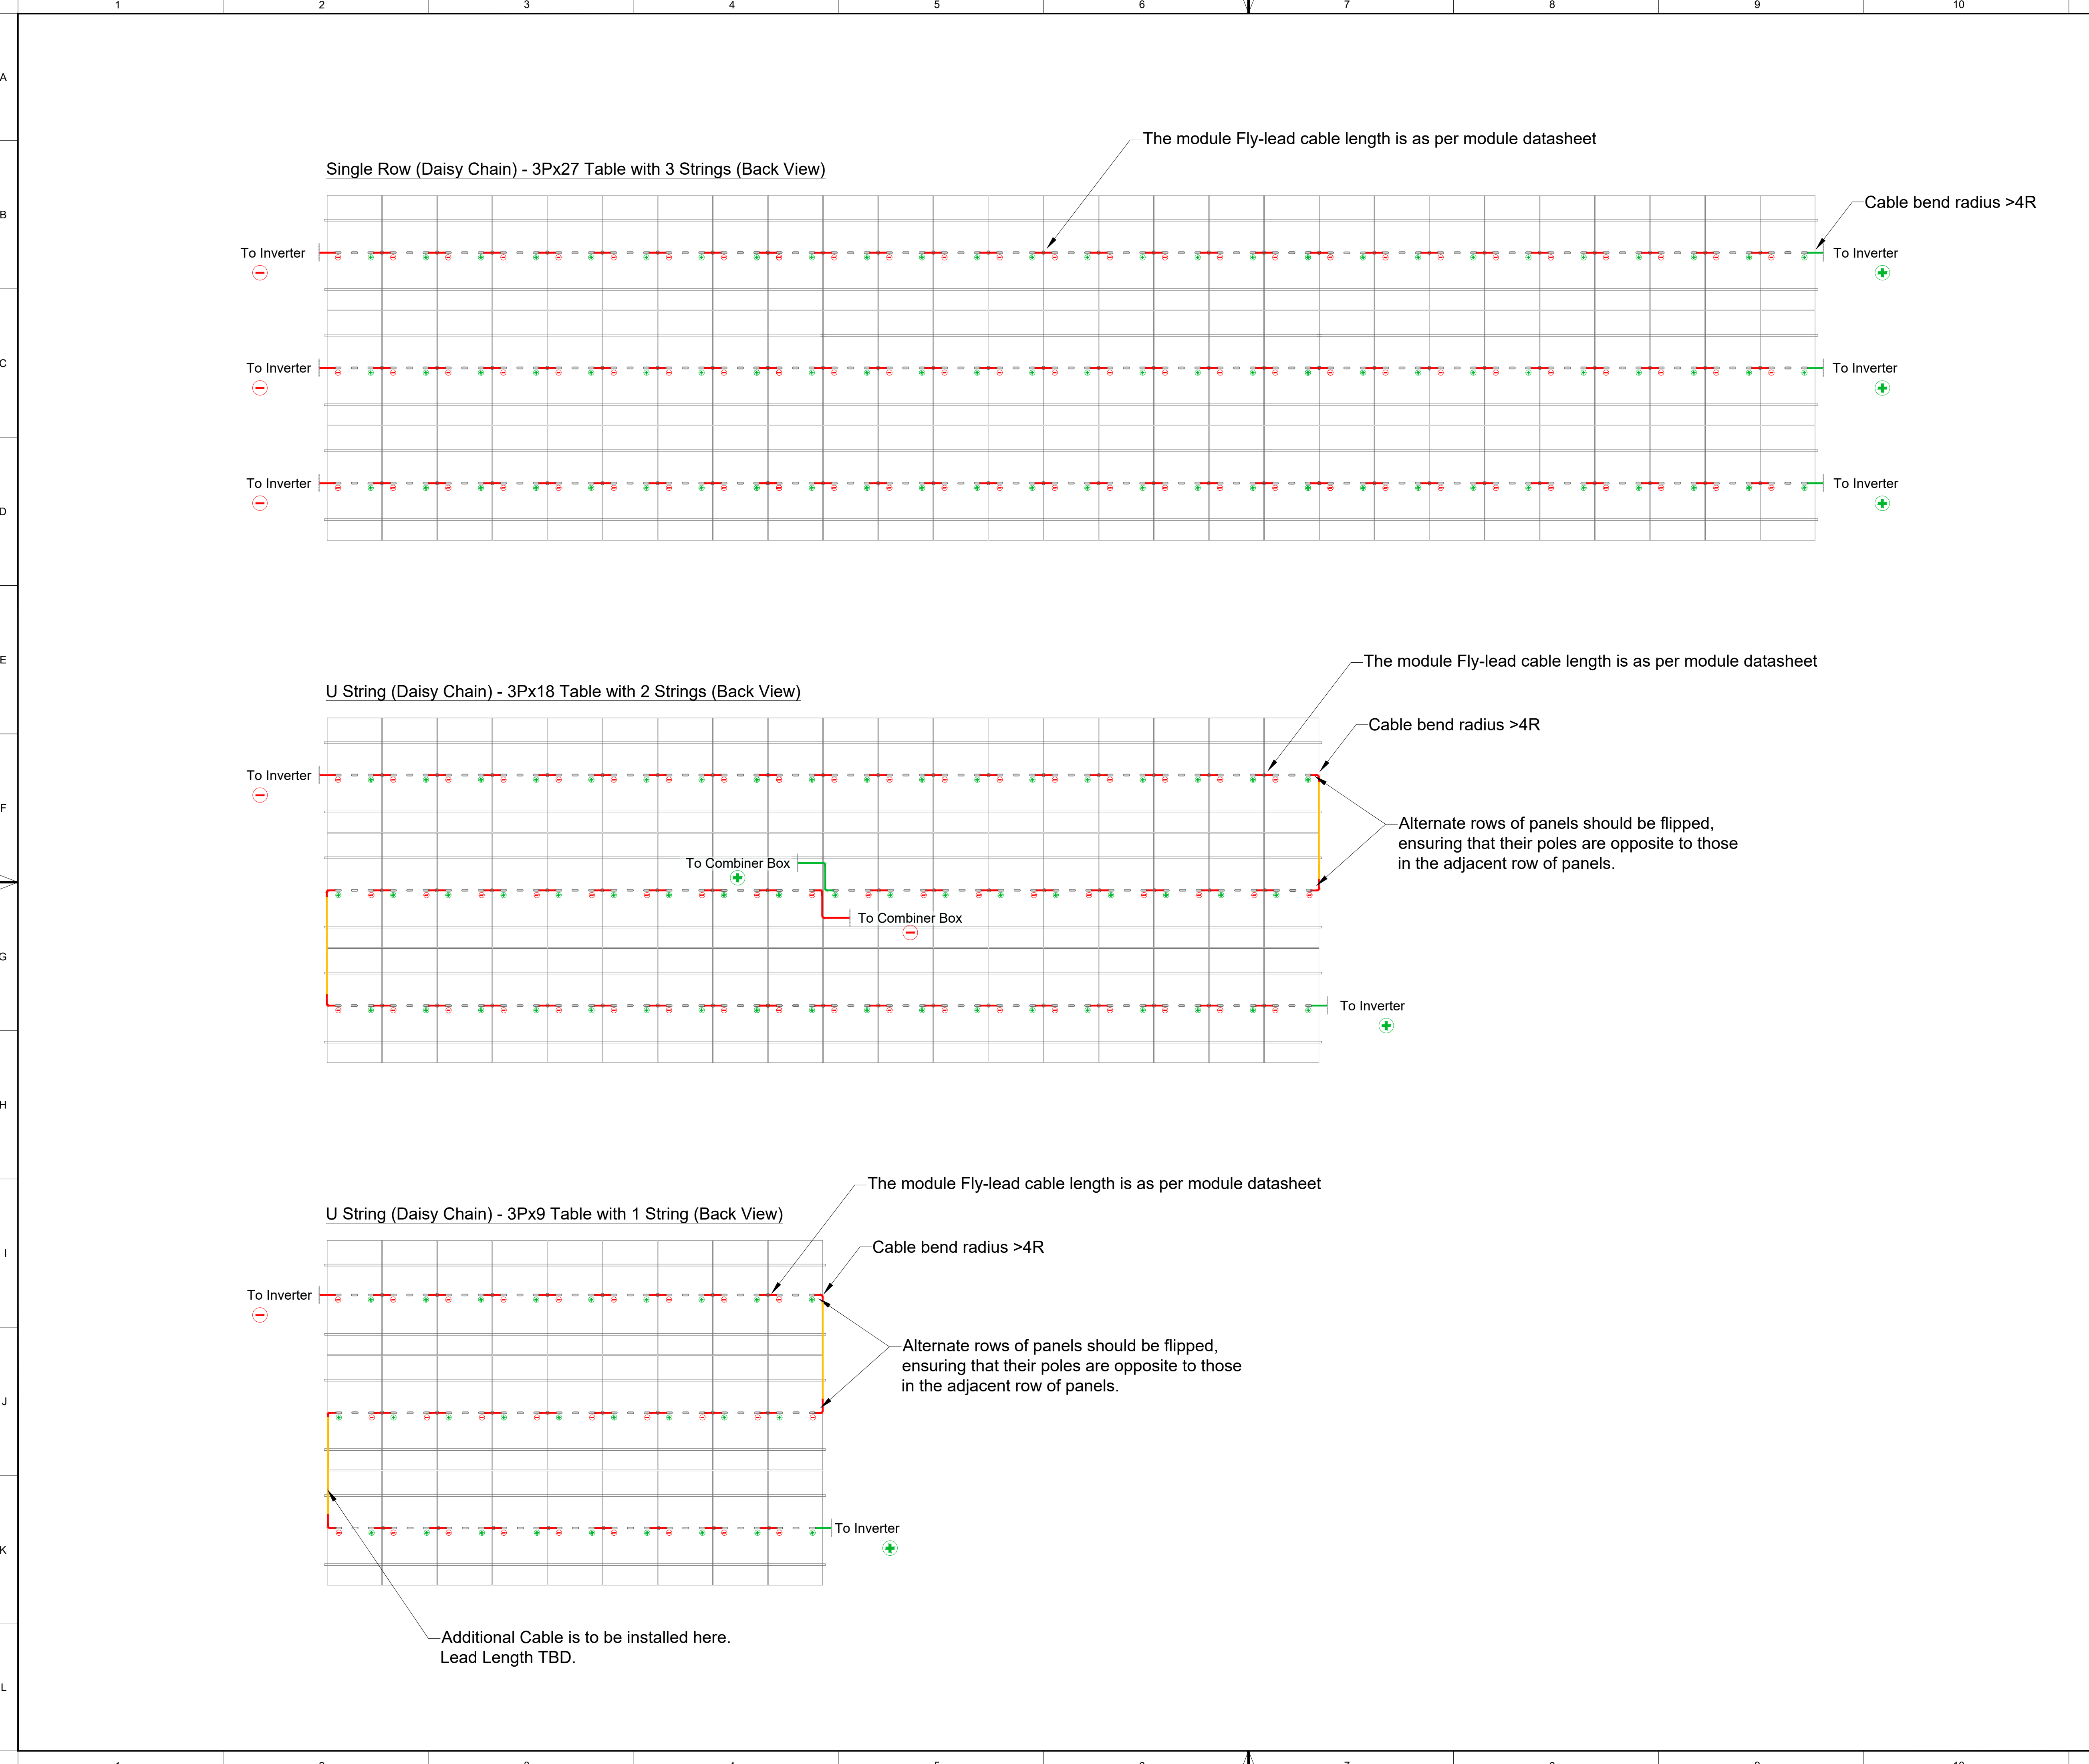

The document is protected by copyright and design rights. Any unauthorized reproduction, distribution, or use constitutes an infringement and may result in legal action.

© Ethical Power Ltd. All rights reserved.

Do not scale from this drawing.

NOTES

- THIS DRAWING TO BE READ IN CONJUNCTION WITH ALL RELEVANT ENGINEERS AND SPECIALISTS DRAWINGS & SPECIFICATIONS.
- ANY DISCREPANCIES BETWEEN THIS DRAWING AND ANY OTHER TO BE REPORTED TO THE ENGINEER IMMEDIATELY.
- ALL WORKS TO COMPLY WITH THE MOST CURRENT BRITISH STANDARDS.
- ALL DIMENSIONS IN MILLIMETERS UNLESS STATED OTHERWISE. NO DIMENSIONS ARE TO BE SCALED OFF THE DRAWING. USE FIGURED DIMENSIONS ONLY.
- ALL DIMENSIONS TO BE $\pm 3\text{mm}$ UNLESS SPECIFIED OTHERWISE.

Reference Drawings:

EP-EC006-GA-1 (General Arrangement)

Reference Documents:

JAM66D45 LB 640W (PV Module Datasheet)

Site Details:

	Model	Rating	Qty	Total Capacity	
Modules	JAM72D45-620/LB	640Wp	76815 (total) 2845 string 0 Modules Ballasted	49.16MWp	
Inverter	SG350HX	352kVA	125	44MVA	
TX Station	MVS3200	3520kVA	3	46.46MVA	
	MVS4480	4928kVA	3		
	MVS6400	7040kVA	3		
Tilt & Pitch		18°			
Nominal Voltage at Connection Point		33kV ICP			
Export Capacity		40MW @0.95 PF			
Import Capacity		335 kVA			

0	First Issued			
	KN	NM	AH	27/03/2026

REV	DESCRIPTION			
	DESIGNED	CHECKED	APPROVED	DATE

ETHICAL POWER LTD.
UNIT 9, DUNCHIDEOCK BARTON,
DUNCHIDEOCK, EXETER
EX2 9UA
(t) 01726 218618
www.ethical-power.com

Project: EC006 - HESSAY

Title: STRING ARRANGEMENT

Drawing Status: PRELIMINARY

Grid Ref (6 fig):

Site address: LOW MOOR LANE,
YORK,
YO268JT

DWG No:	SHEET:	SCALE (A1):	REV:
EP-EC006-STR-1	1 OF 1	NTS	00

PRELIMINARY ISSUE
DRAFT VERSION