


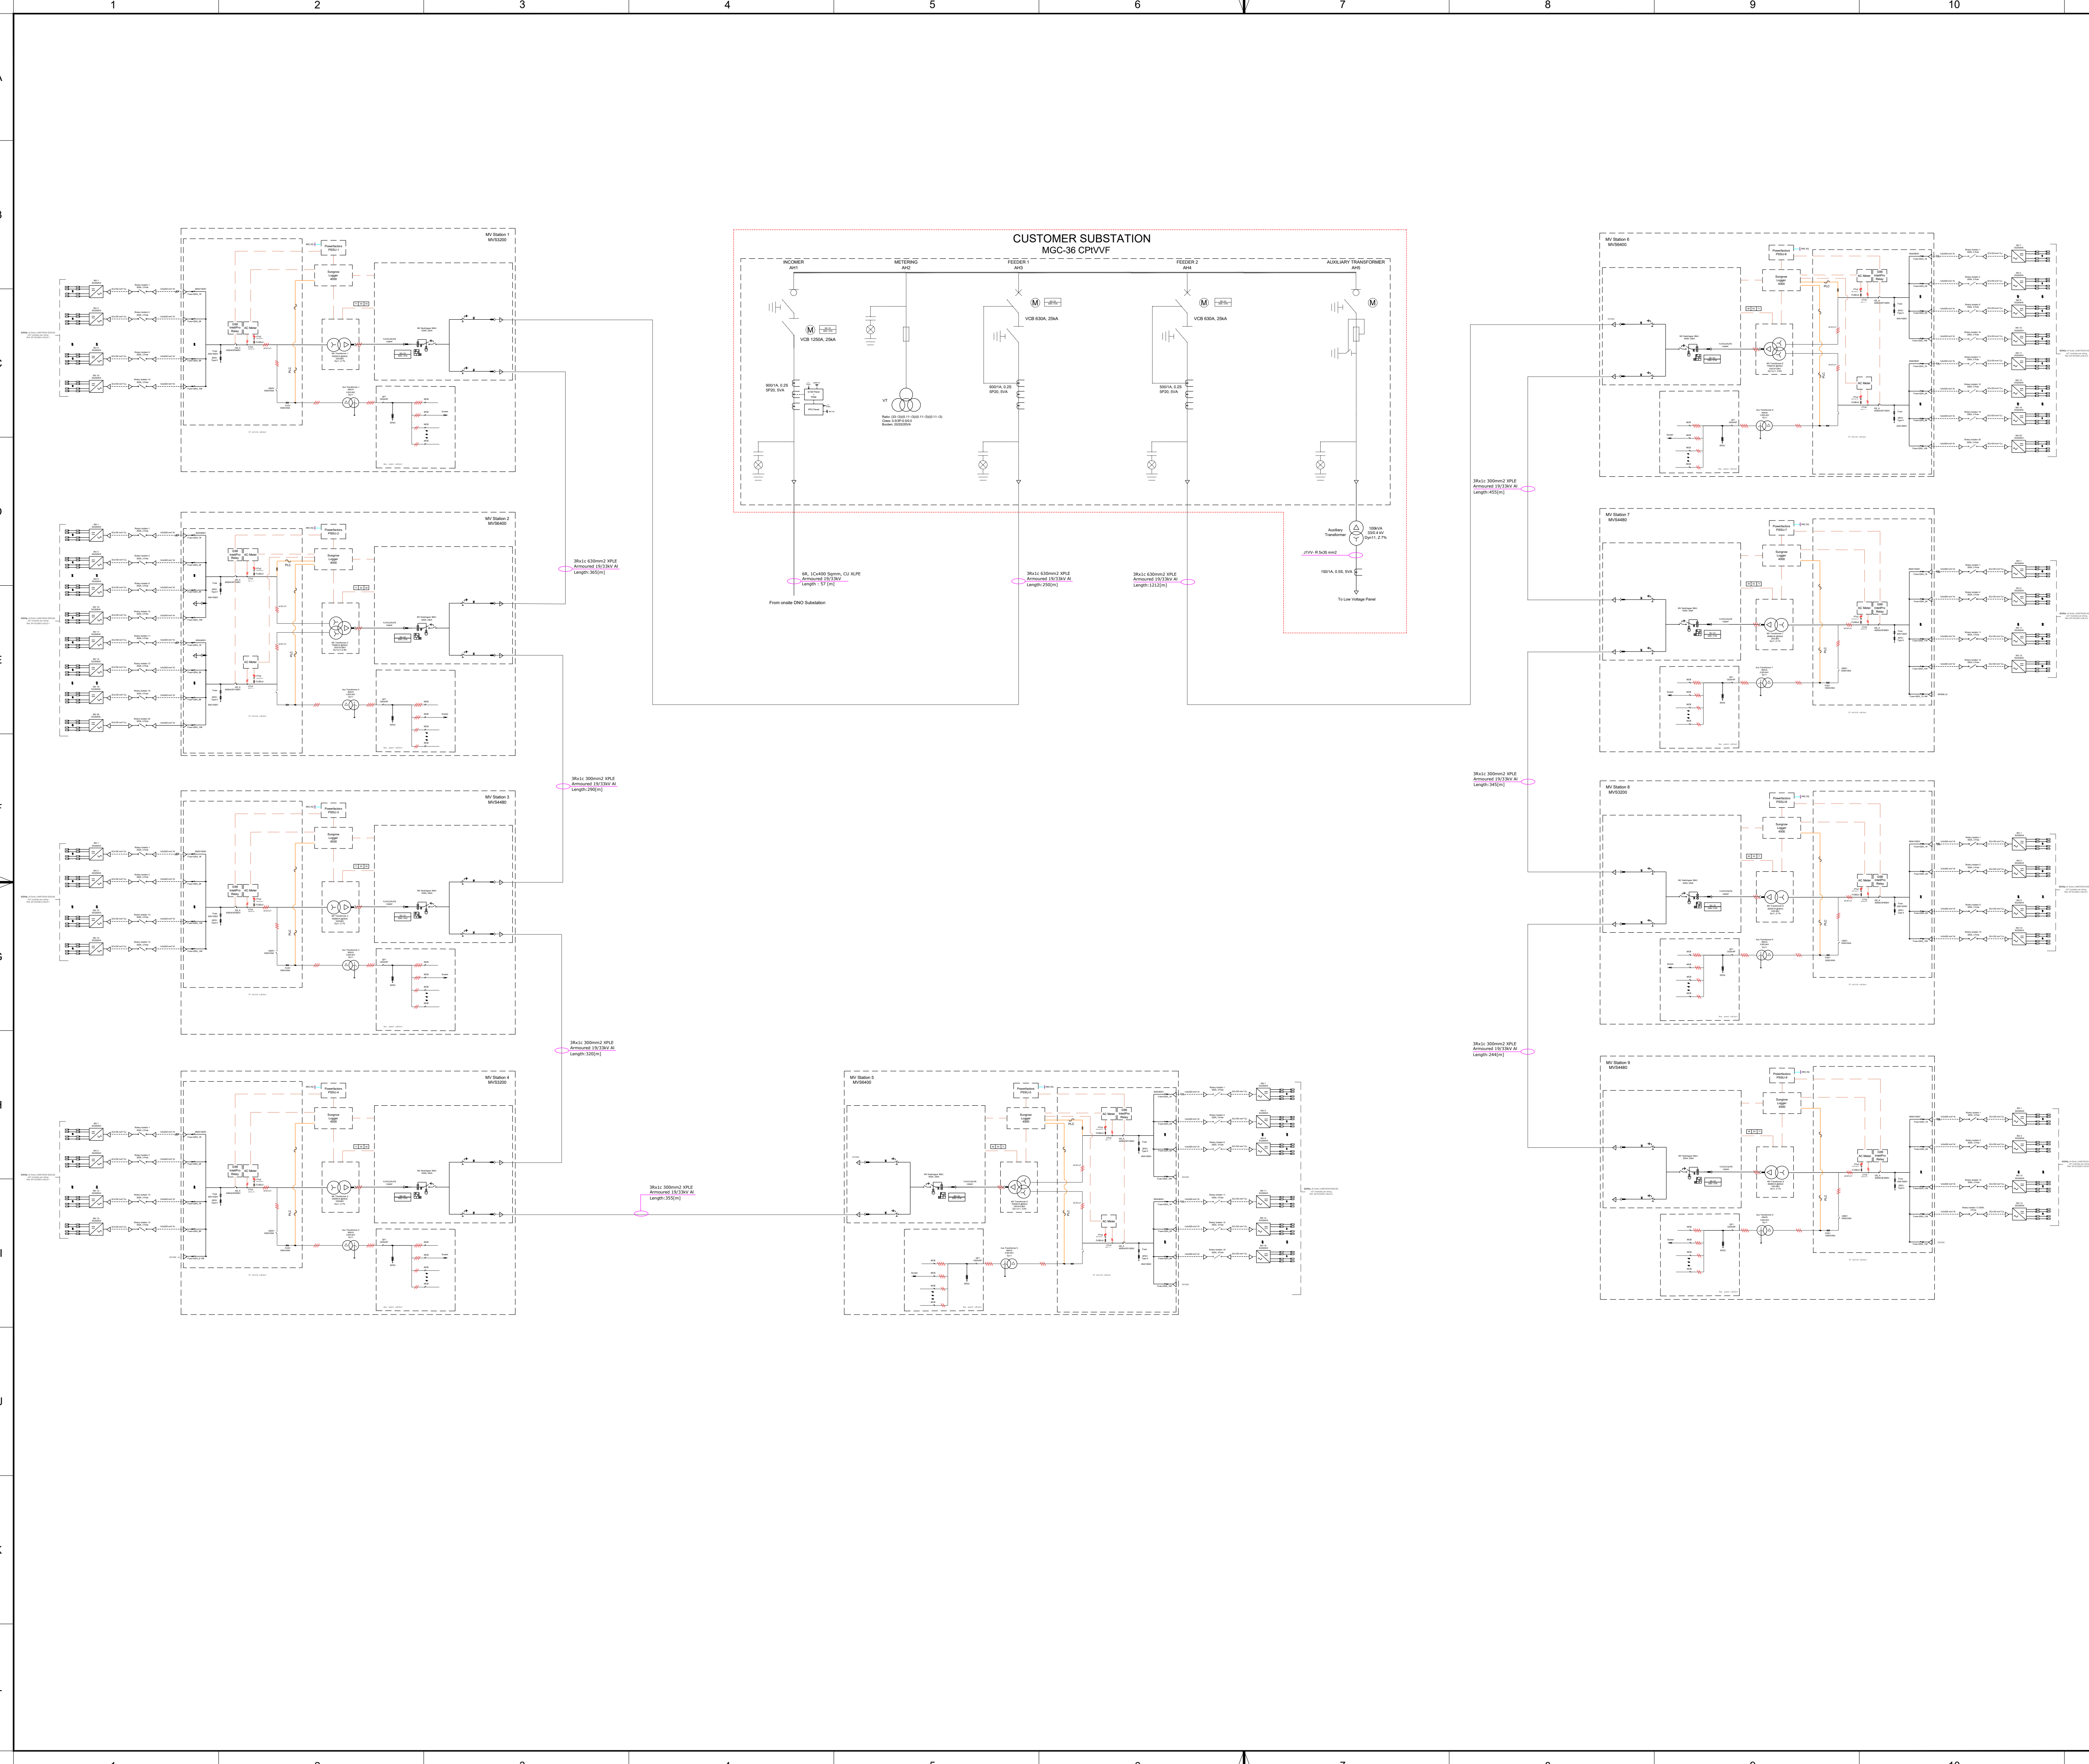

This document is protected by copyright and design rights. Any unauthorised reproduction, distribution, or use constitutes an infringement and may result in legal action. Ethical Power Ltd. All rights reserved.

Do not scale from this drawing.

NOTES

- THIS DRAWING TO BE READ IN CONJUNCTION WITH ALL RELEVANT ENGINEERS AND SPECIALISTS DRAWINGS & SPECIFICATIONS.
- ANY DISCREPANCIES BETWEEN THIS DRAWING AND ANY OTHER TO BE REPORTED TO THE ENGINEER IMMEDIATELY.
- ALL WORKS TO COMPLY WITH THE MOST CURRENT BRITISH STANDARDS.
- ALL DIMENSIONS IN MILLIMETERS UNLESS STATED OTHERWISE. NO DIMENSIONS ARE TO BE SCALED OFF THE DRAWING. USE FIGURED DIMENSIONS ONLY.
- ALL DIMENSIONS TO BE ±3mm UNLESS SPECIFIED OTHERWISE.

Reference Drawings:

EP-EC006 -GA-1 (General Arrangement)

Reference Documents:

DS_20250108_MVS6400-LV_Datasheet_V3_EN (EUR) (STS Datasheet)
DS_20240312_SG350HX_Datasheet_V21_EN (Inverter Datasheet)
JAM72D45 LB 620W (PV Module Datasheet)

Site Details:

	Model	Rating	Qty	Total Capacity
Modules	JAM72D45-620/LB	620Wp	80001 (total)	49.6MWp
			2963 string	
			0	
			Modules Ballasted	
Inverter	SG350HX	352kVA	125	44MVA
TX Station	MVS3200	3520kVA	3	46.46MVA
	MVS4480	4928kVA	3	
	MVS6400	7040kVA	3	
Tilt & Pitch	15°			
Nominal Voltage at Connection Point	33kV ICP			
Export Capacity	40MW @0.95 PF			
Import Capacity	335 kVA			

1	SLD Updated			
	KN	NB	AH	24/03/2026
0	First Issued			
	KN	NB	AH	13/03/2026
REV	DESCRIPTION			
	DESIGNED	CHECKED	APPROVED	DATE



ETHICAL POWER LTD.
UNIT 9, DUNCHIDEOCK BARTON,
DUNCHIDEOCK, EXETER
EX2 9JA
(t) 01726 218618
www.ethical-power.com

Project:

EC006 - HESSAY

Title:

GENERAL SLD

Drawing Status:

PRELIMINARY

Grid Ref (6 fig):

Site address:

LOW MOOR LANE,
YORK,
YO26 6JT

DWG No:	SHEET:	SCALE (A1):	REV:
EP-EC006-SLD-1	1 OF 1	NTS	00

**PRELIMINARY ISSUE
DRAFT VERSION**