


Stratigraphy of internal roads
Flat ground

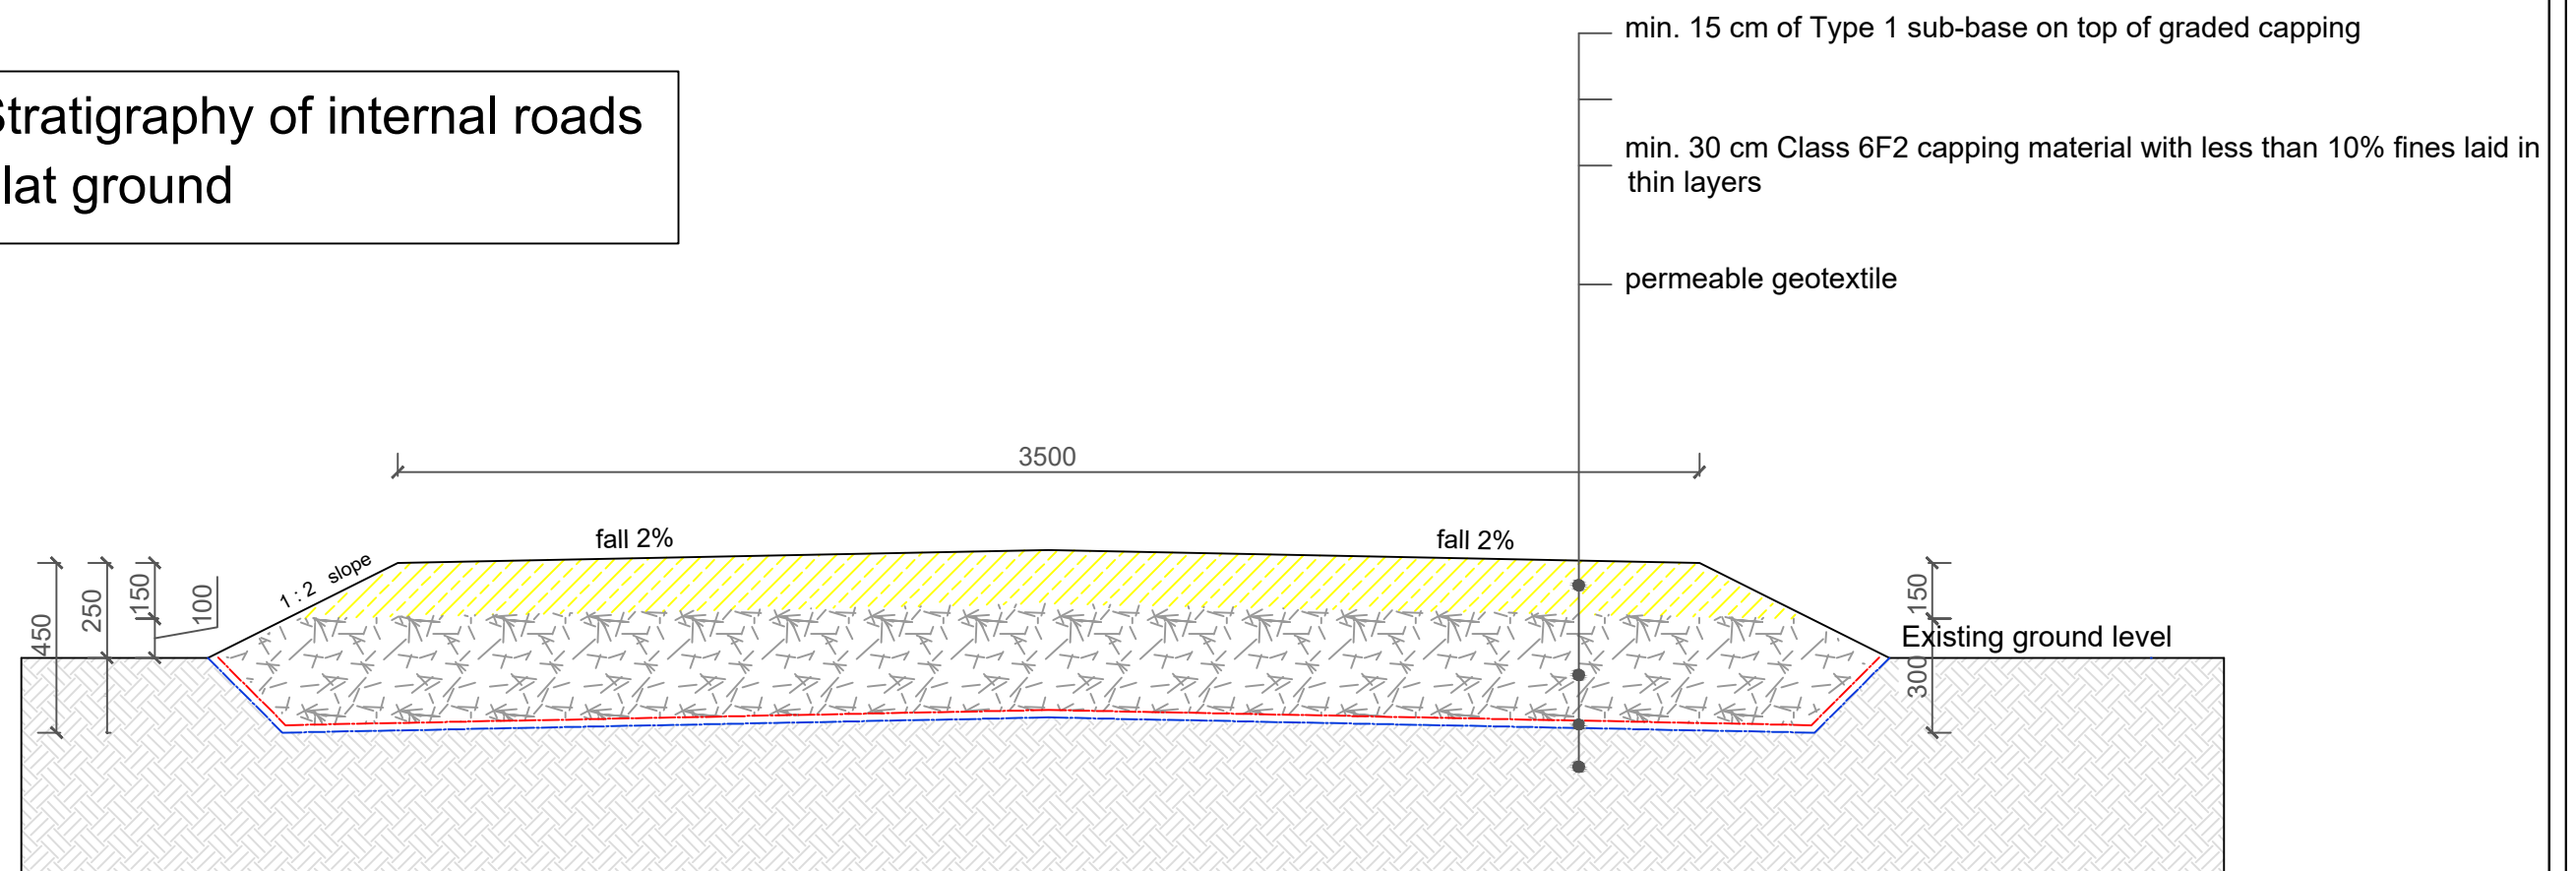

REV	DATE	DESCRIPTION
1	10/10/2024	ISSUED FOR
DRAWING TITLE: Road Cross Section		
DRAWING NUMBER: 105-007A-230214		
PROJECT NAME AND ADDRESS: Hessay Solar farm, United Kingdom		
DESIGNER NAME: [Redacted]		
APPROVAL SIGNATURE: [Redacted]		
SCALE: 1:20		
SHEET: A3		
STATUS: Preliminary		
PAGE: 1/1		