


CABLE TRENCH SECTION

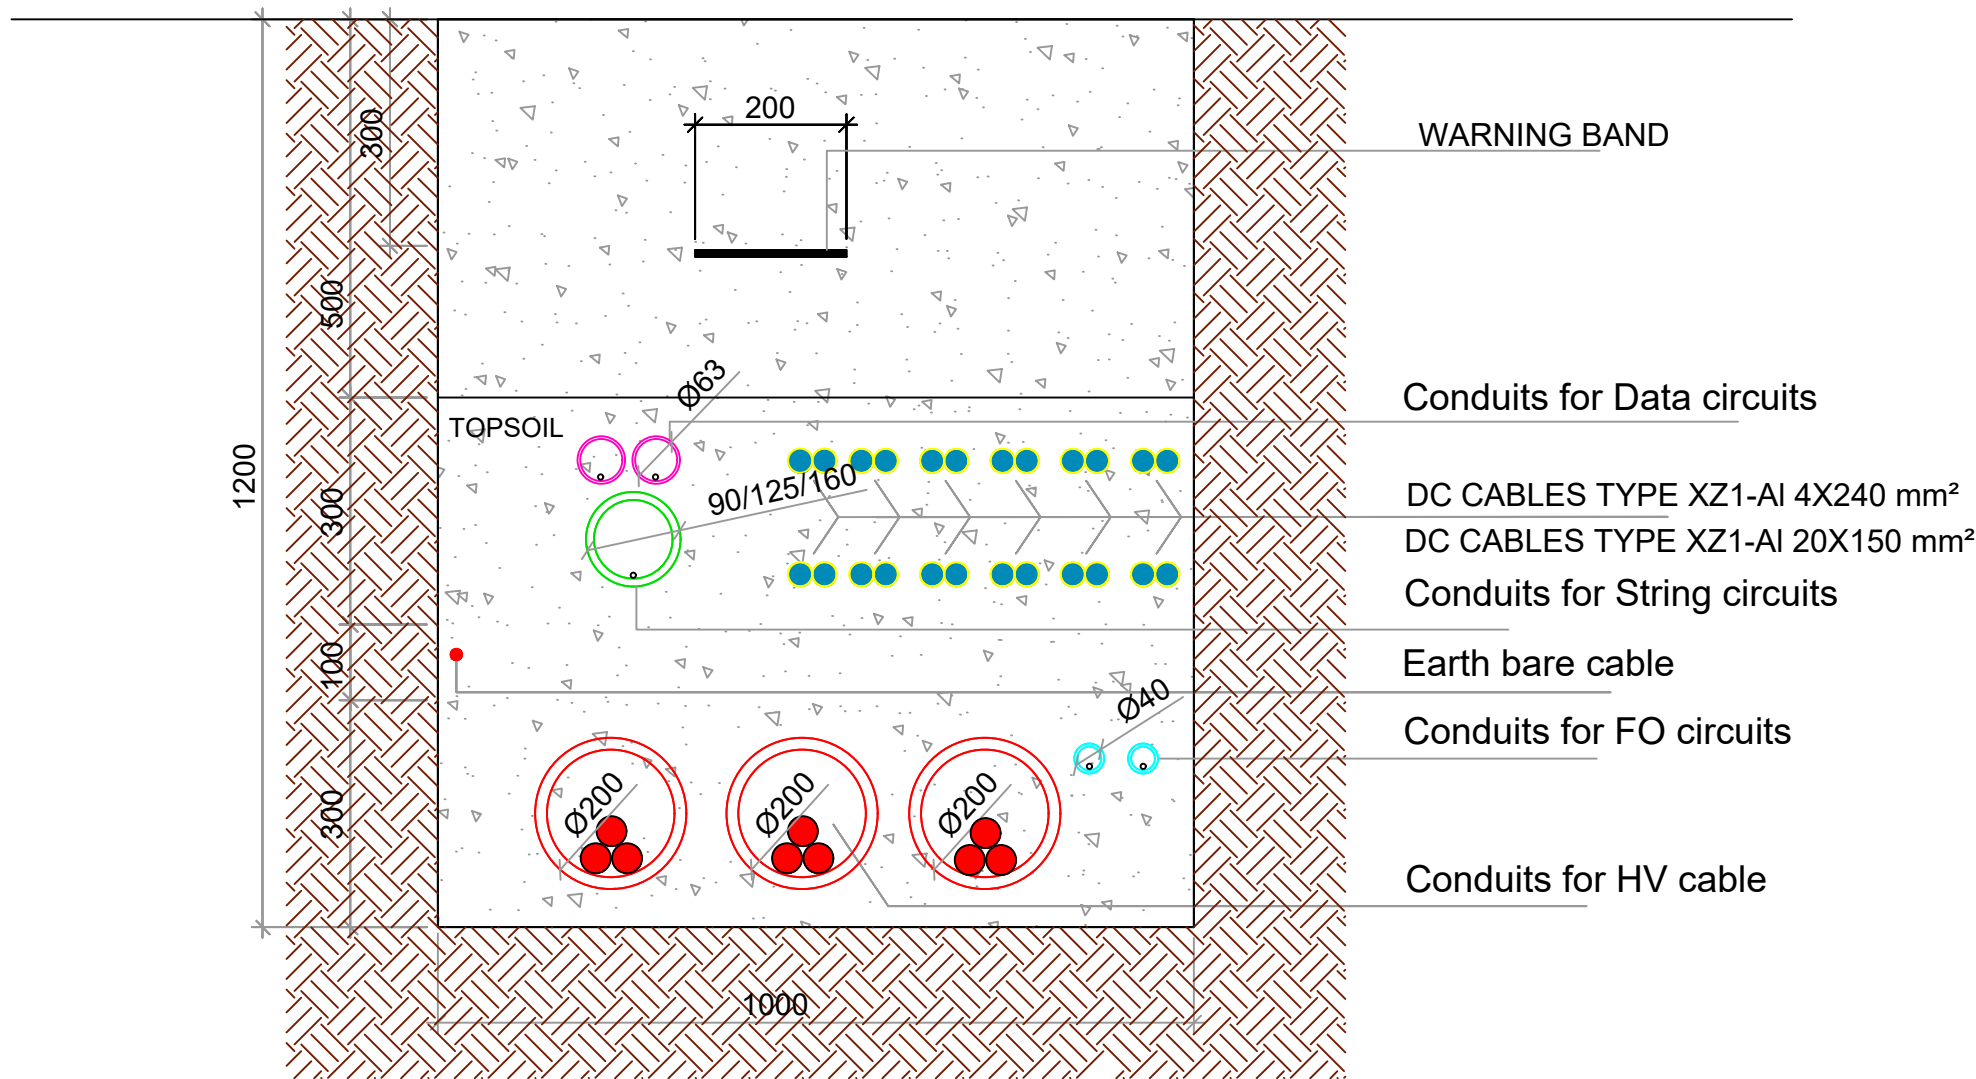

TYPICAL

REV	1	2024-11
DESCRIPTION	Cable Trench Cross Section	105-005A-230214
PROJECT NAME AND ADDRESS	Hessay solar farm United Kingdom	APPROVAL STATUS
DATE	1:10	SCALE
STATUS	Preliminary	1/1